


ALL THAT GLITS



THE SITE

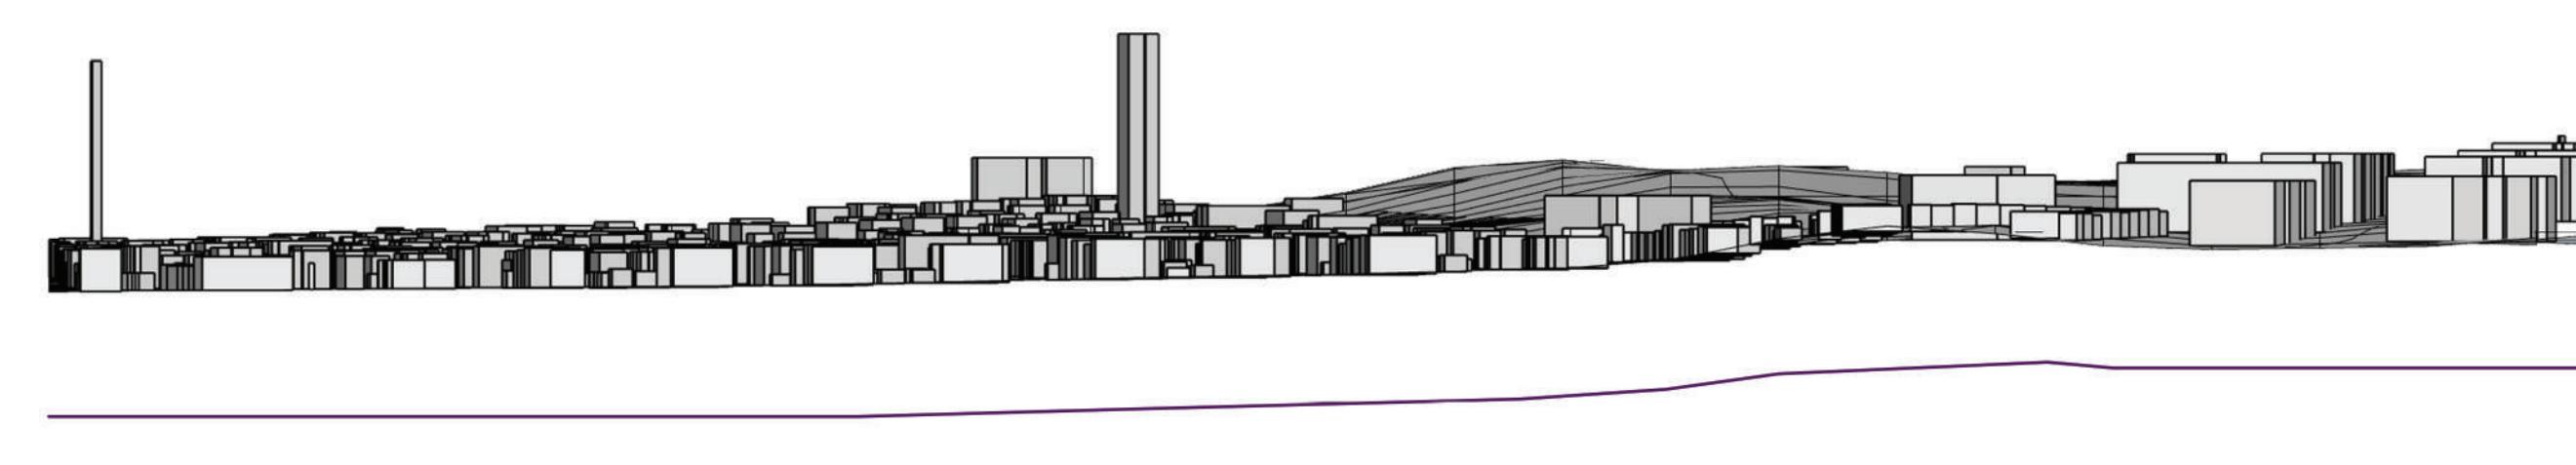

90-06 PARK LANE SOUTH, QUEENS, NY 11421



CHANGEABLE PERCEPTION


Through the creation of a flexible, multifunctional and interconnected sequence of space, changeable perception of volumes, surfaces and materiality are investigated and derived from the manipulation of the given space.

Inspired by the adaptive permanence of queer body, the space performs as a common space which embraces and at the same time engages and joins the community, defining the relation between visual and physical environment, the sensory experience of the body and the emotional experience of the mind.


In terms of materiality, the project aims to capture the spirit of permeability, the sense of lightness through light, the appeal of contrasts, for a sustainable and inclusive way to live.




Main door - Water color

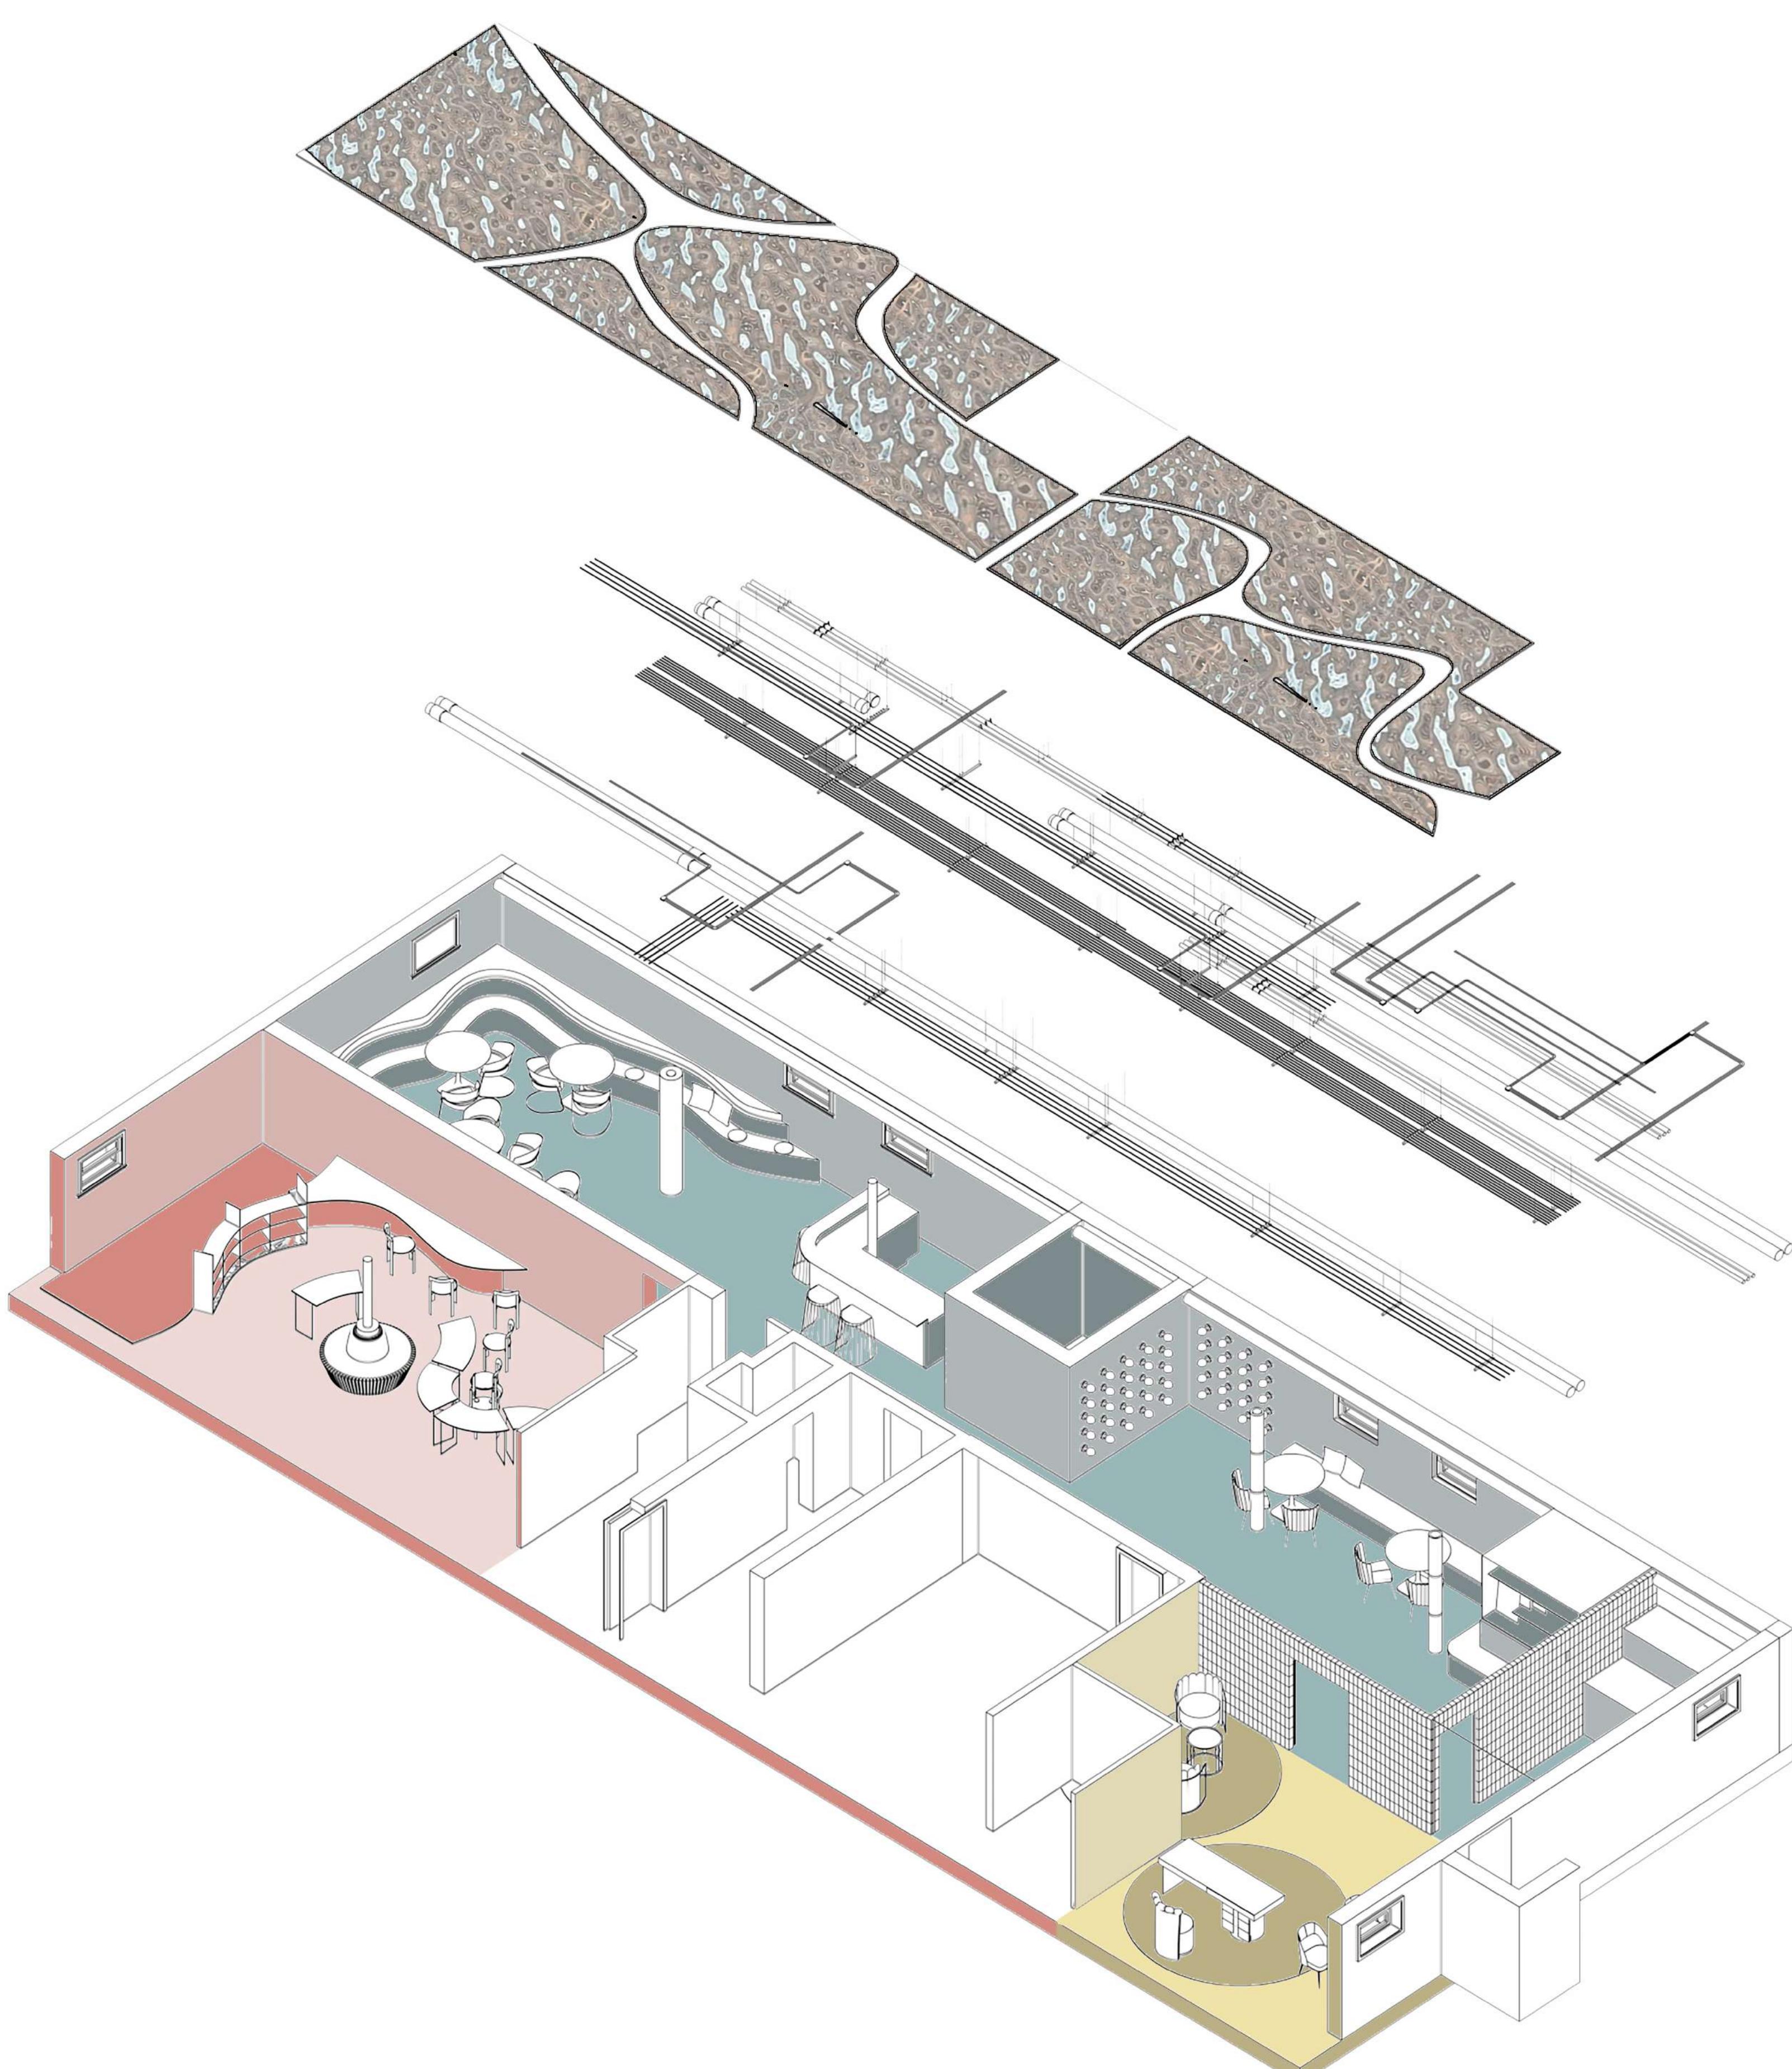


EXPLODED AXO

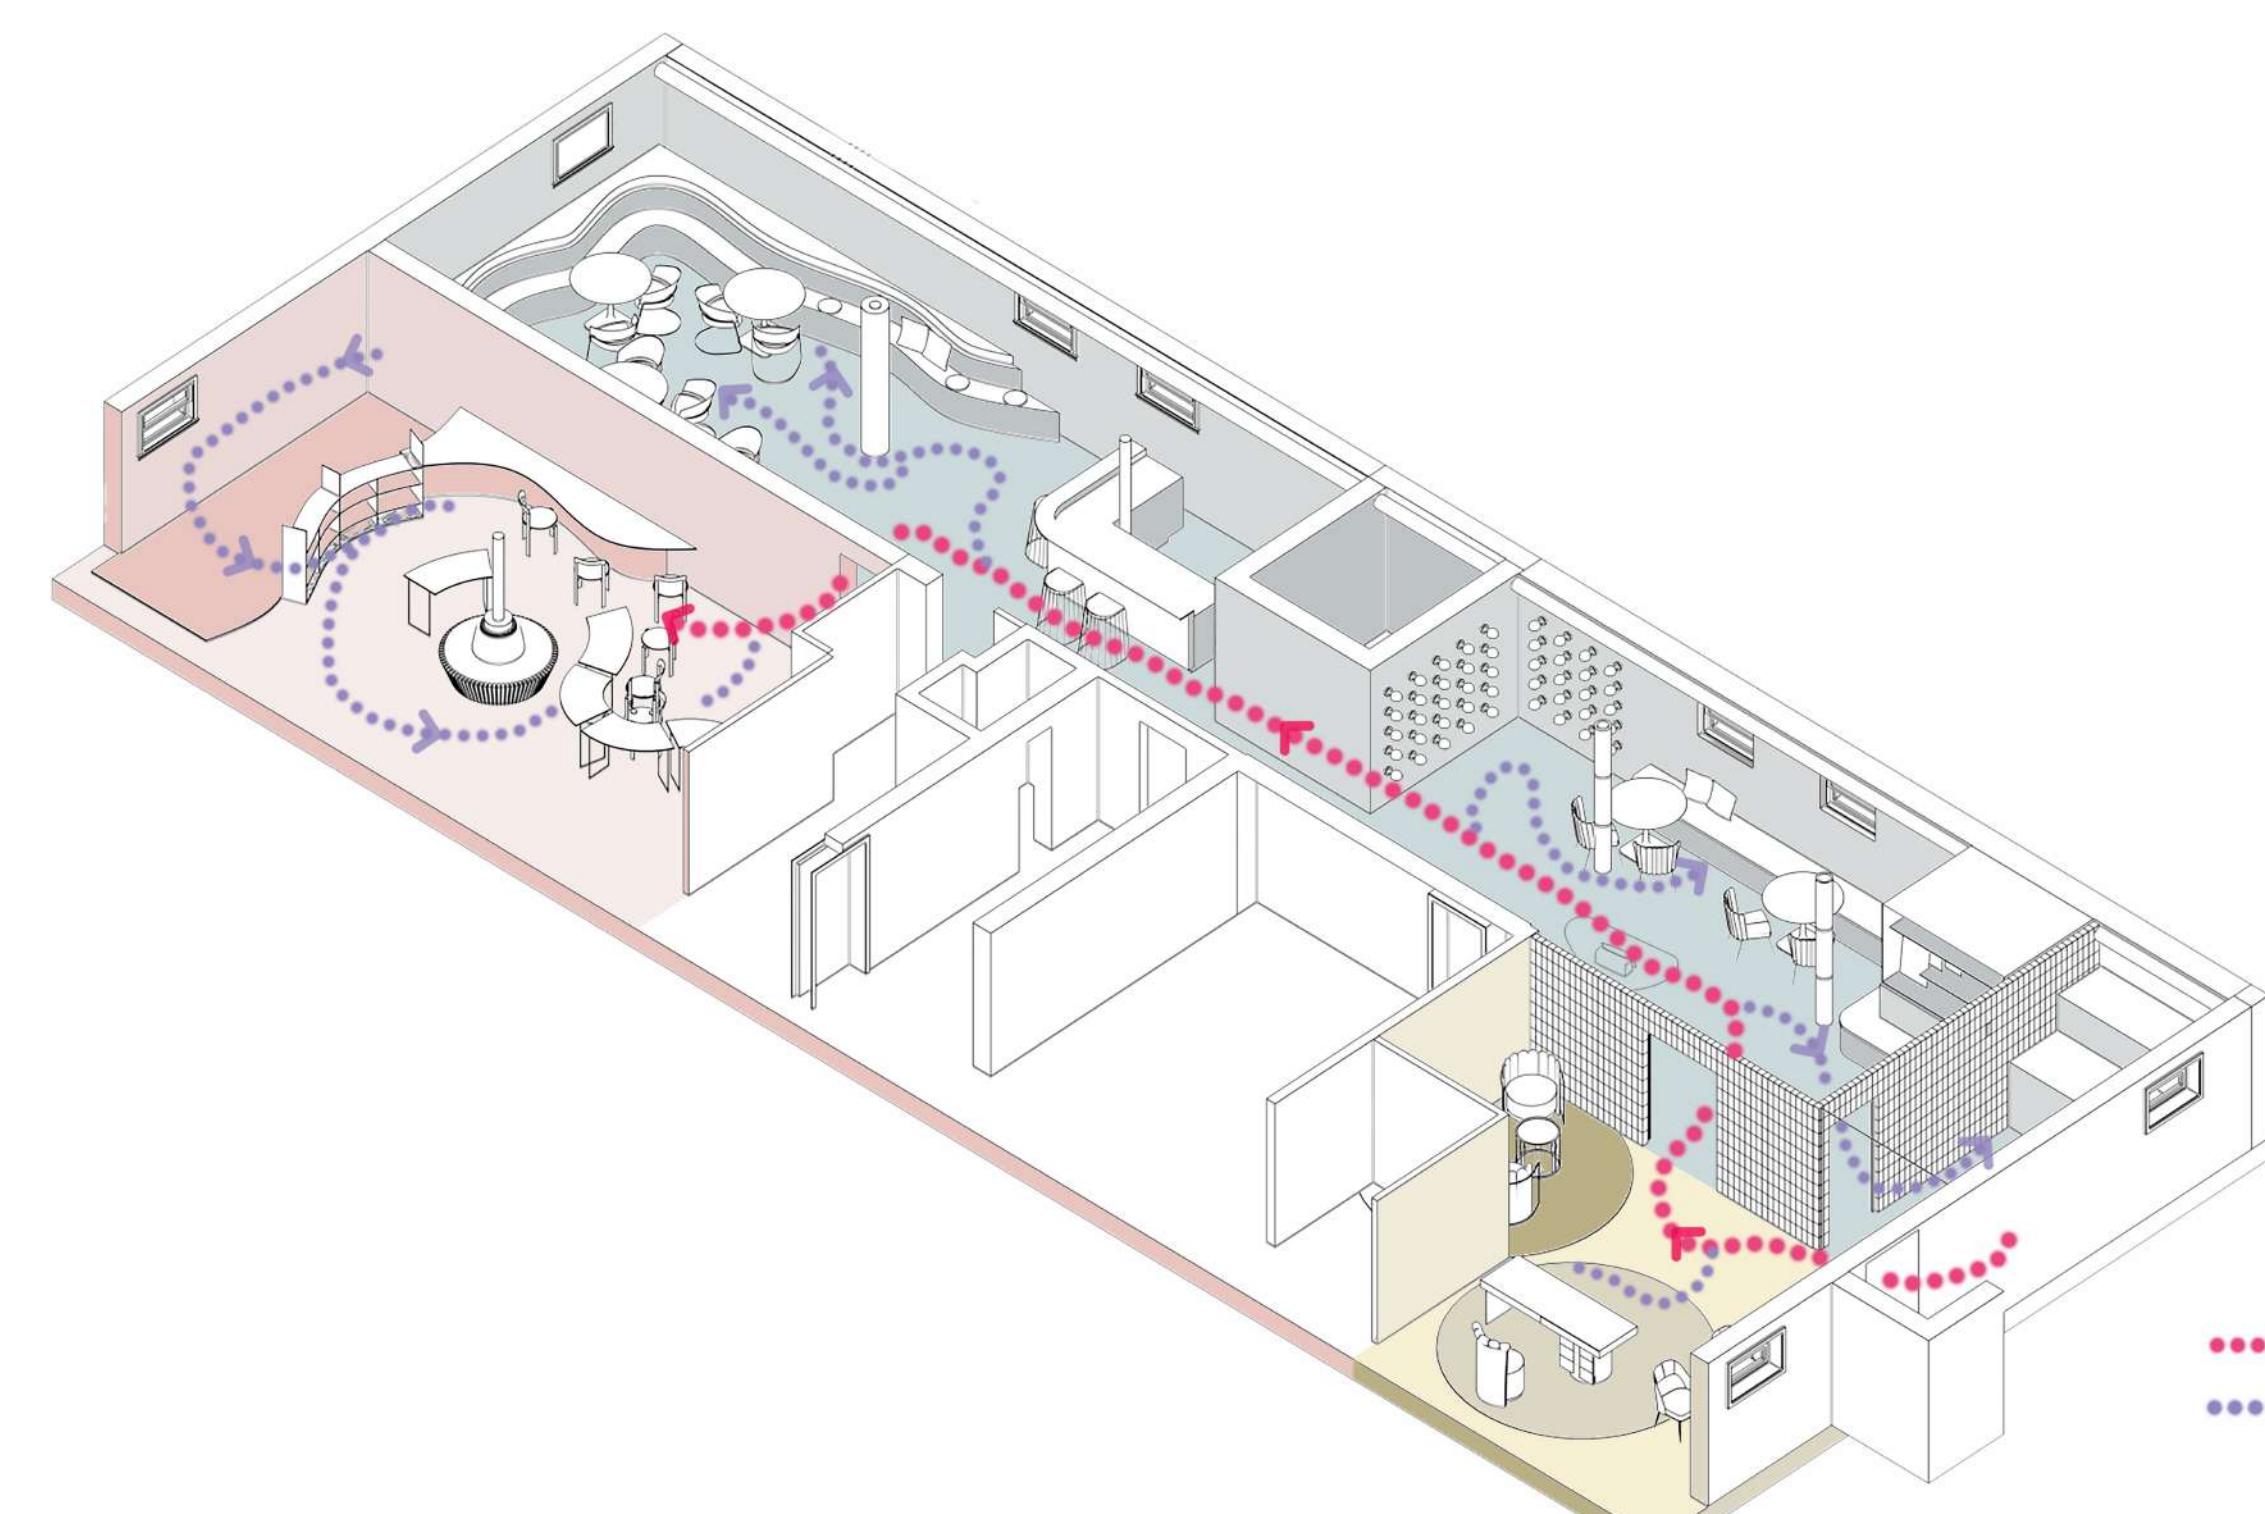

CIRCULATION

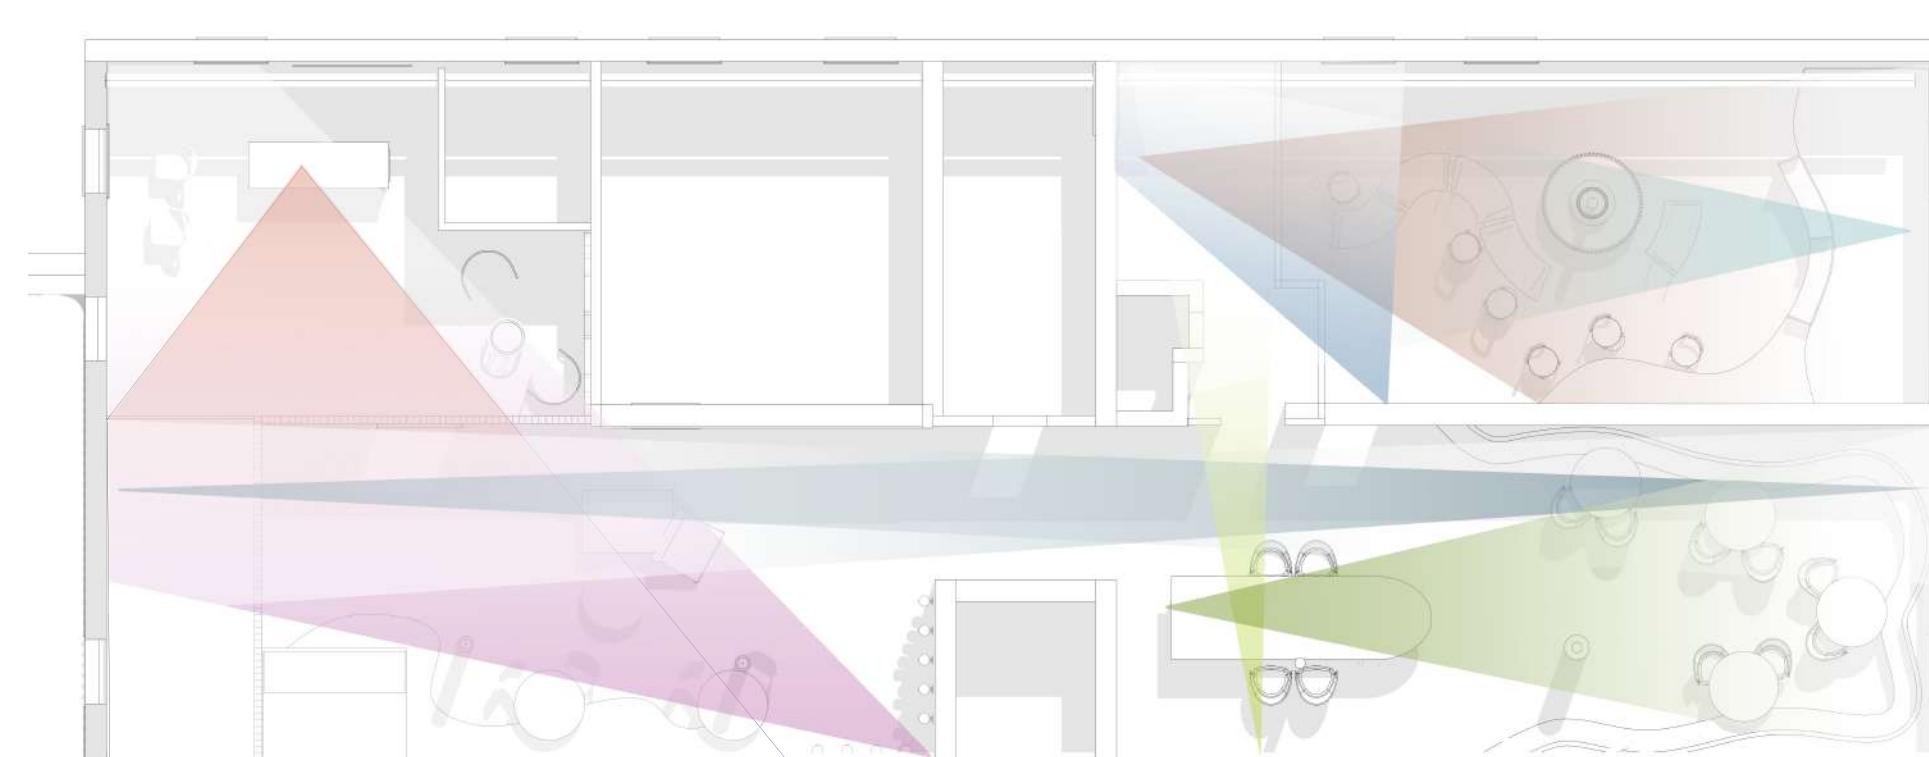

Open spaces together with translucent and transparent materials help to expand the visual field

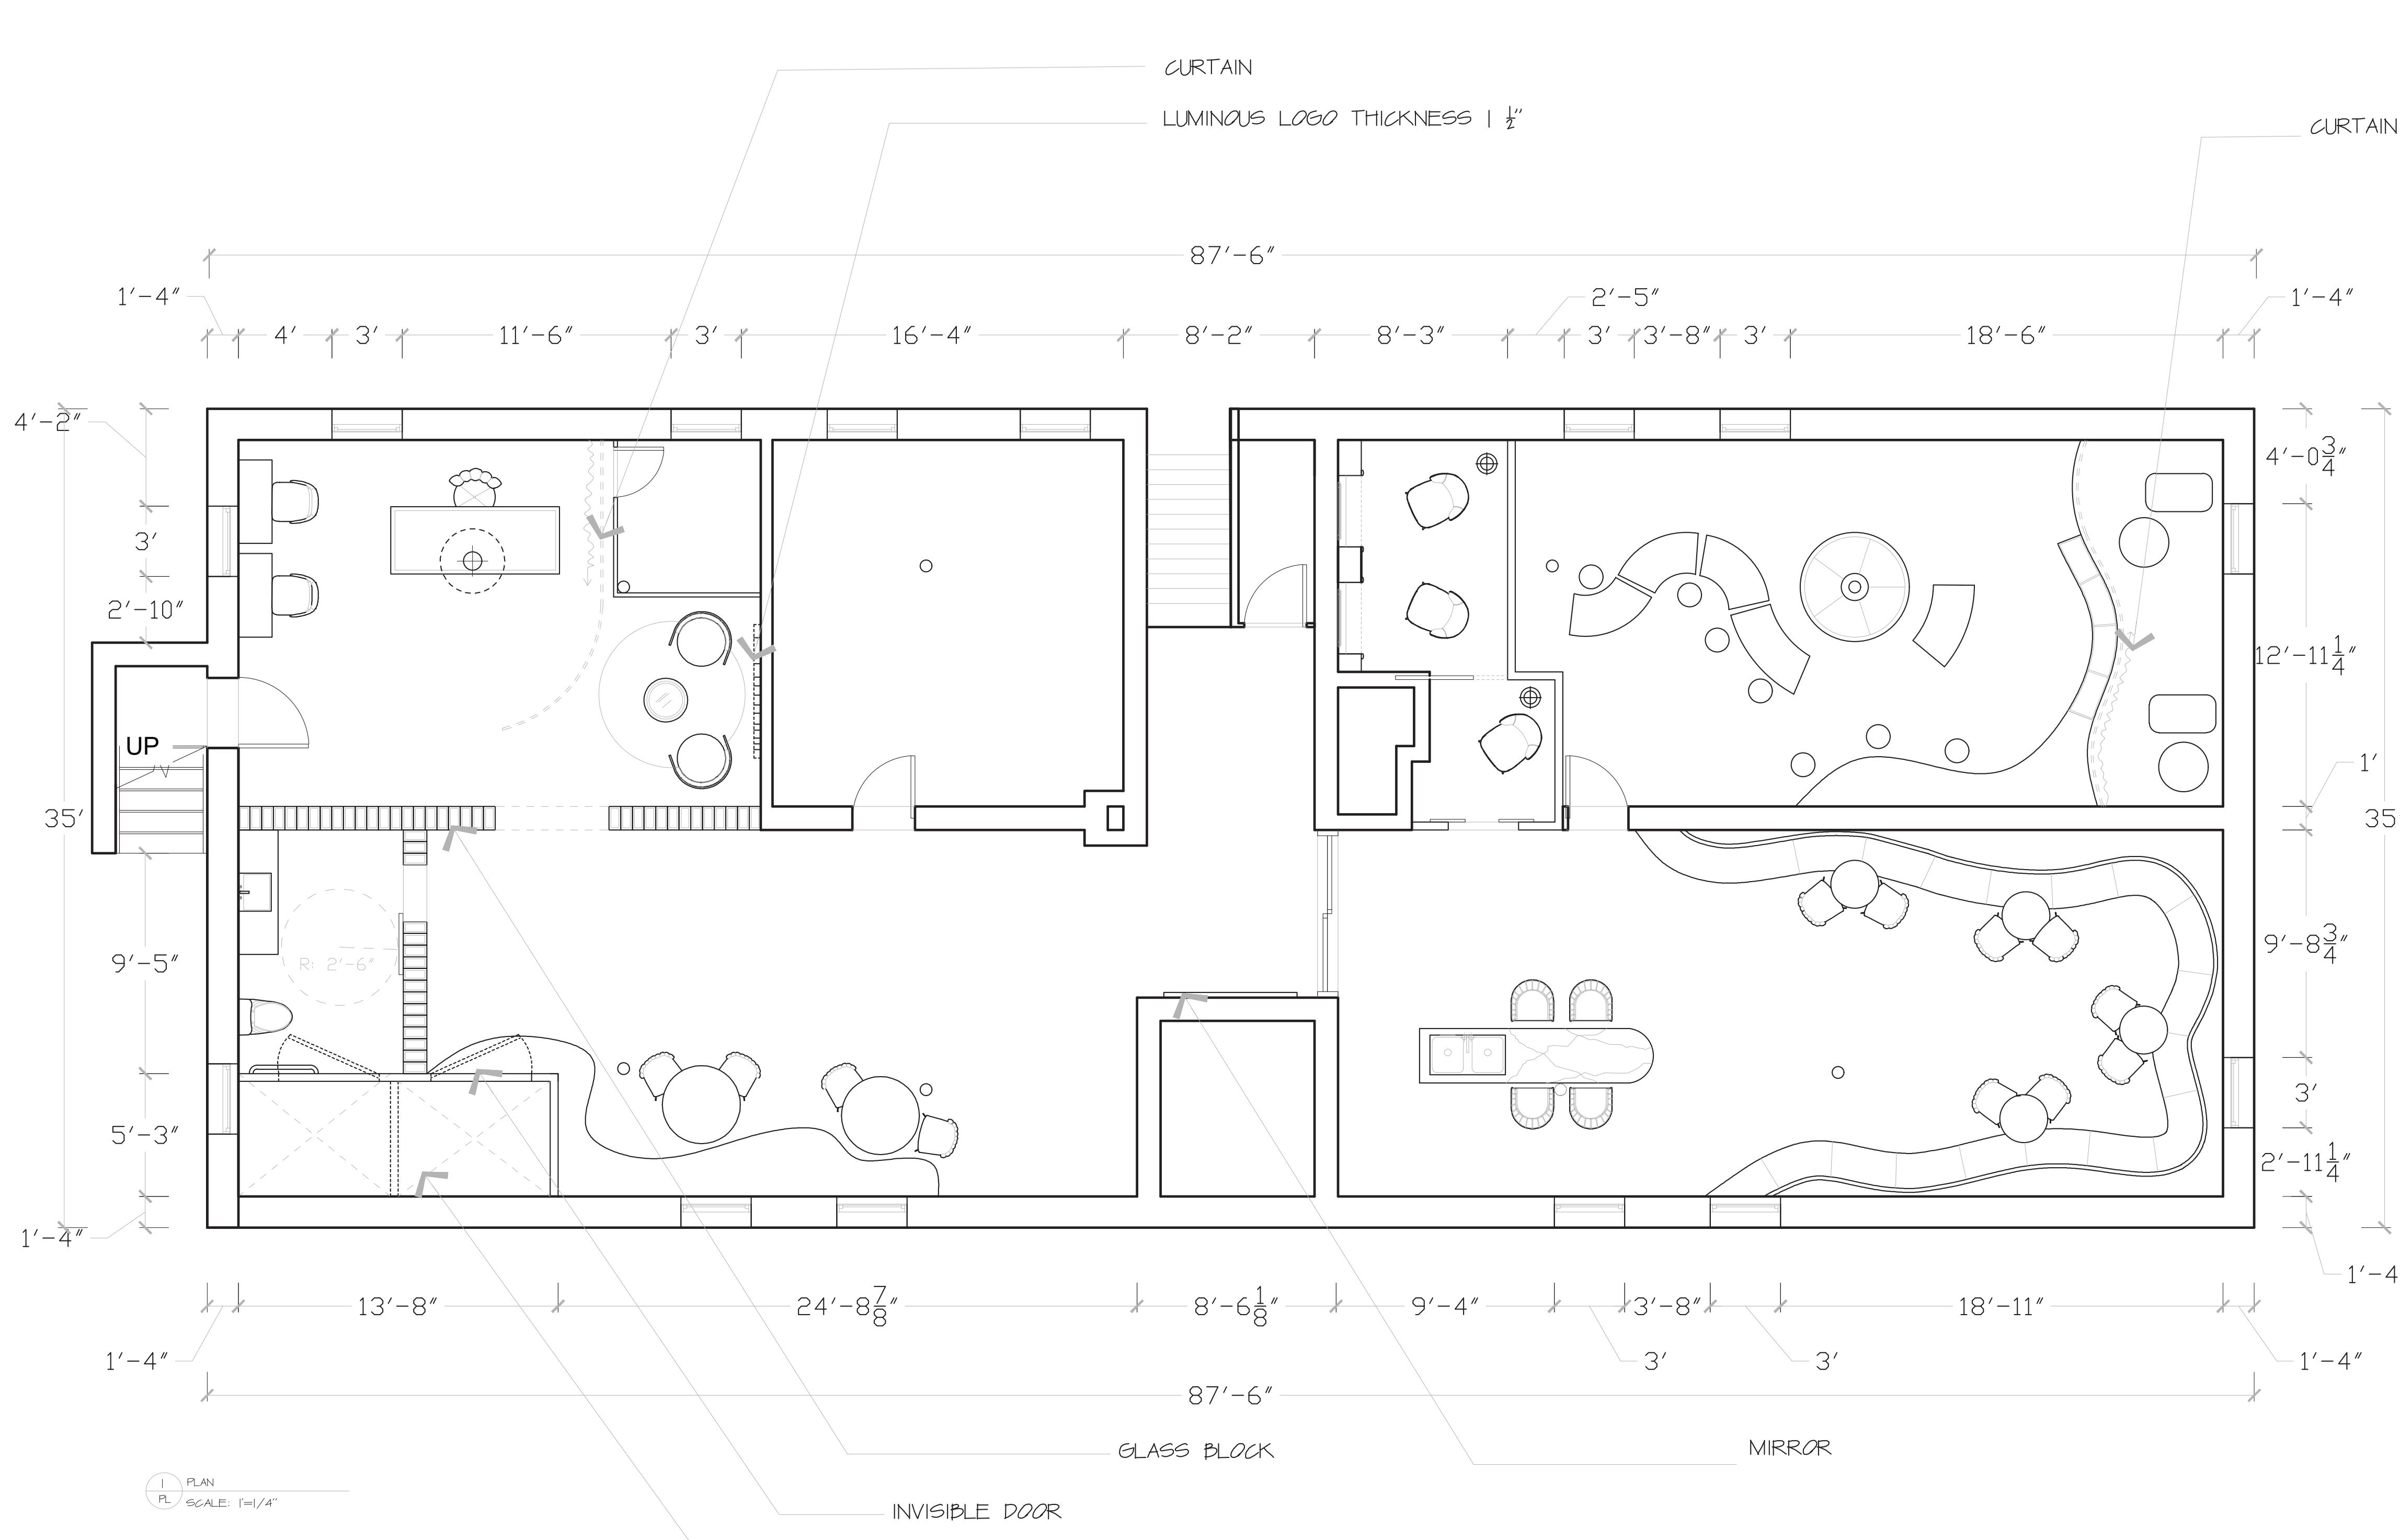

The image displays a 5x3 grid of colored squares. The colors transition through various shades of teal, blue, purple, and green. The top row consists of dark teal squares. The second row contains squares that are lighter teal or blue. The third row features squares with a purple hue. The fourth row shows squares that are more greenish-blue. The bottom row consists of light mint green squares. Each square is a uniform color and has a thin white border separating it from the others.

© 2014 Pearson Education, Inc.


RES



MIR



GLOSSY PAINT

Digitized by srujanika@gmail.com


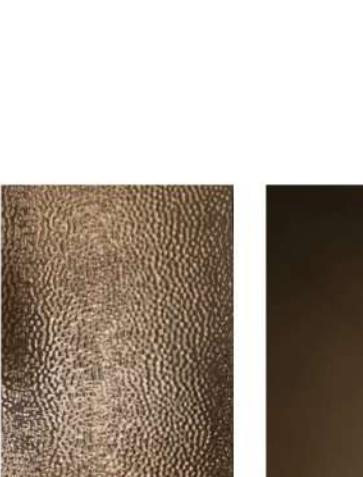


A photograph showing a large stack of gold bars, likely bullion, arranged in a grid pattern. The bars are rectangular and have a distinct yellow-gold color. They are stacked in approximately 5 rows by 8 columns, creating a grid-like structure. The lighting highlights the metallic texture of the bars.

Enhance reflectivity
Blur the boundaries
Enlarge the space

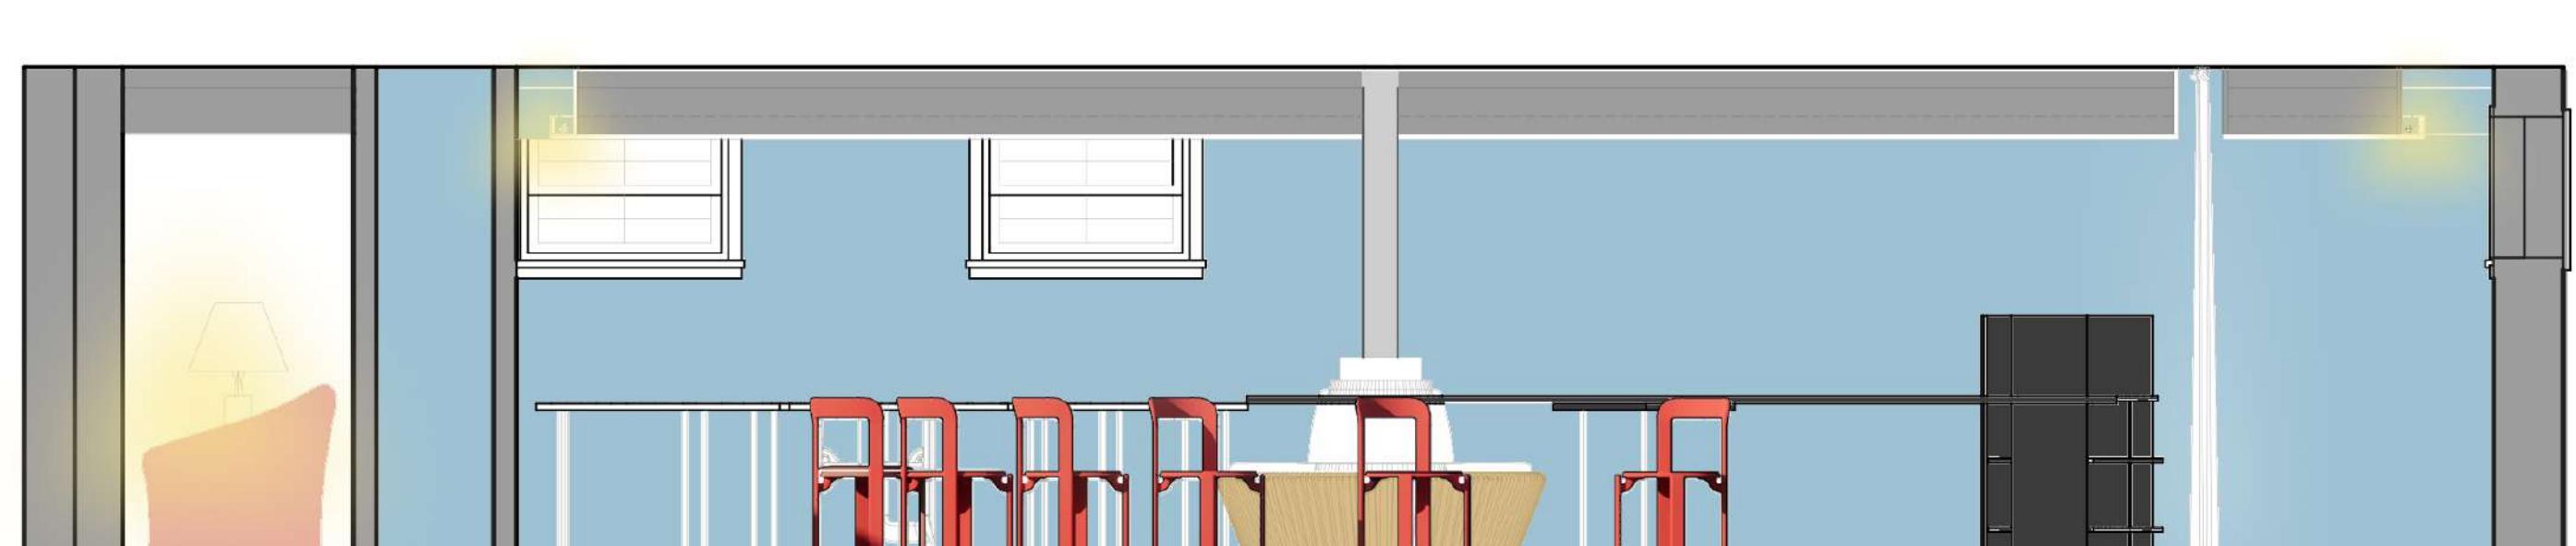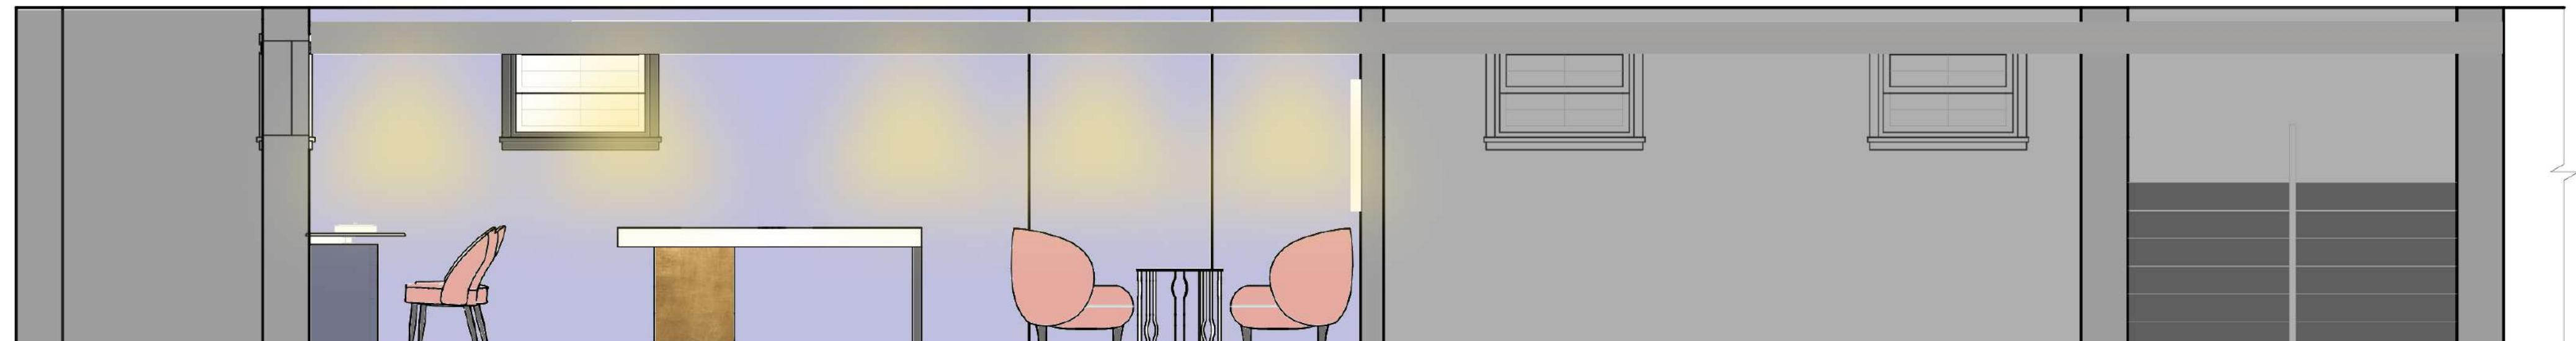


ELEVATION A-A' 1/4": 1'0"

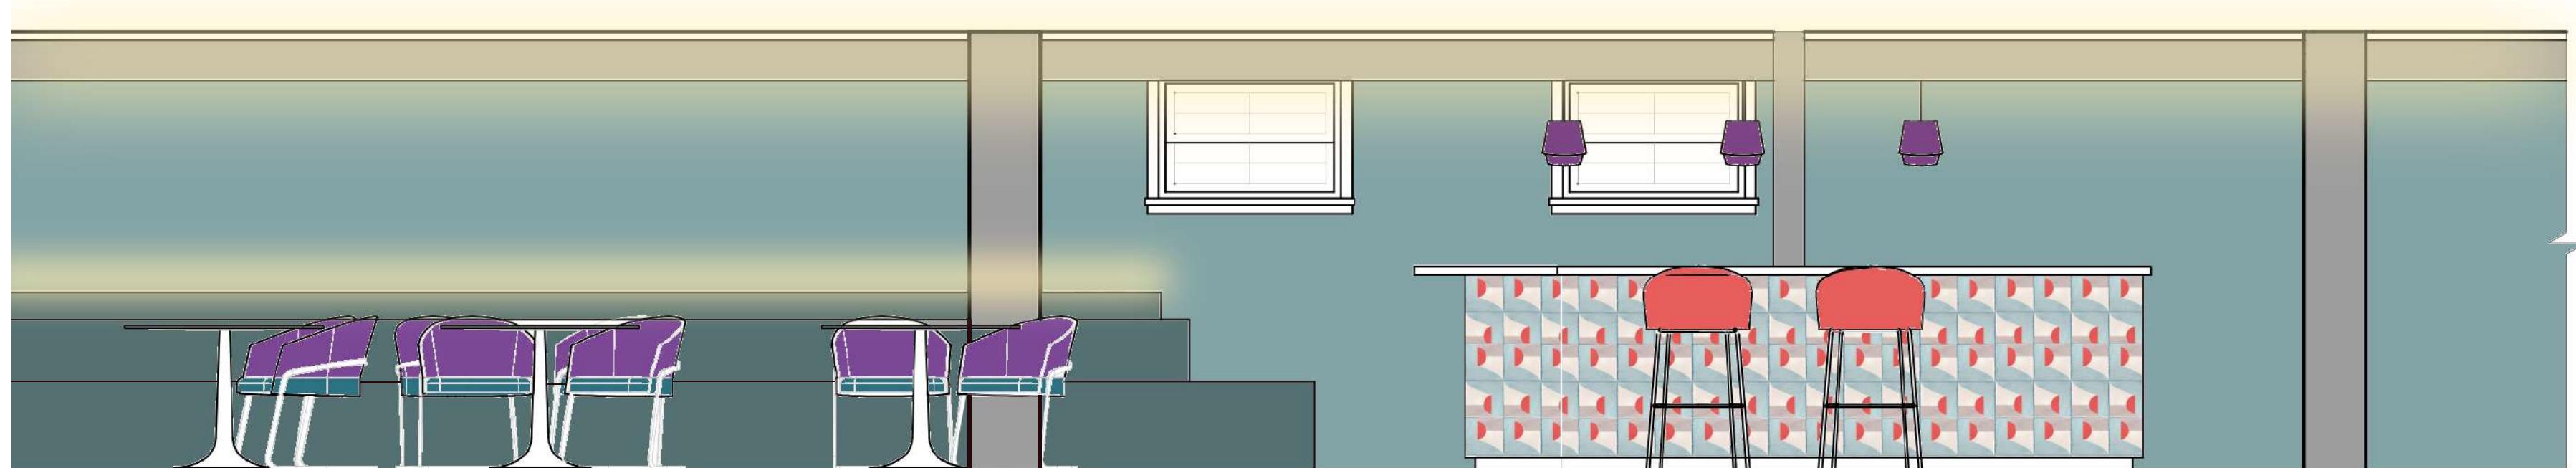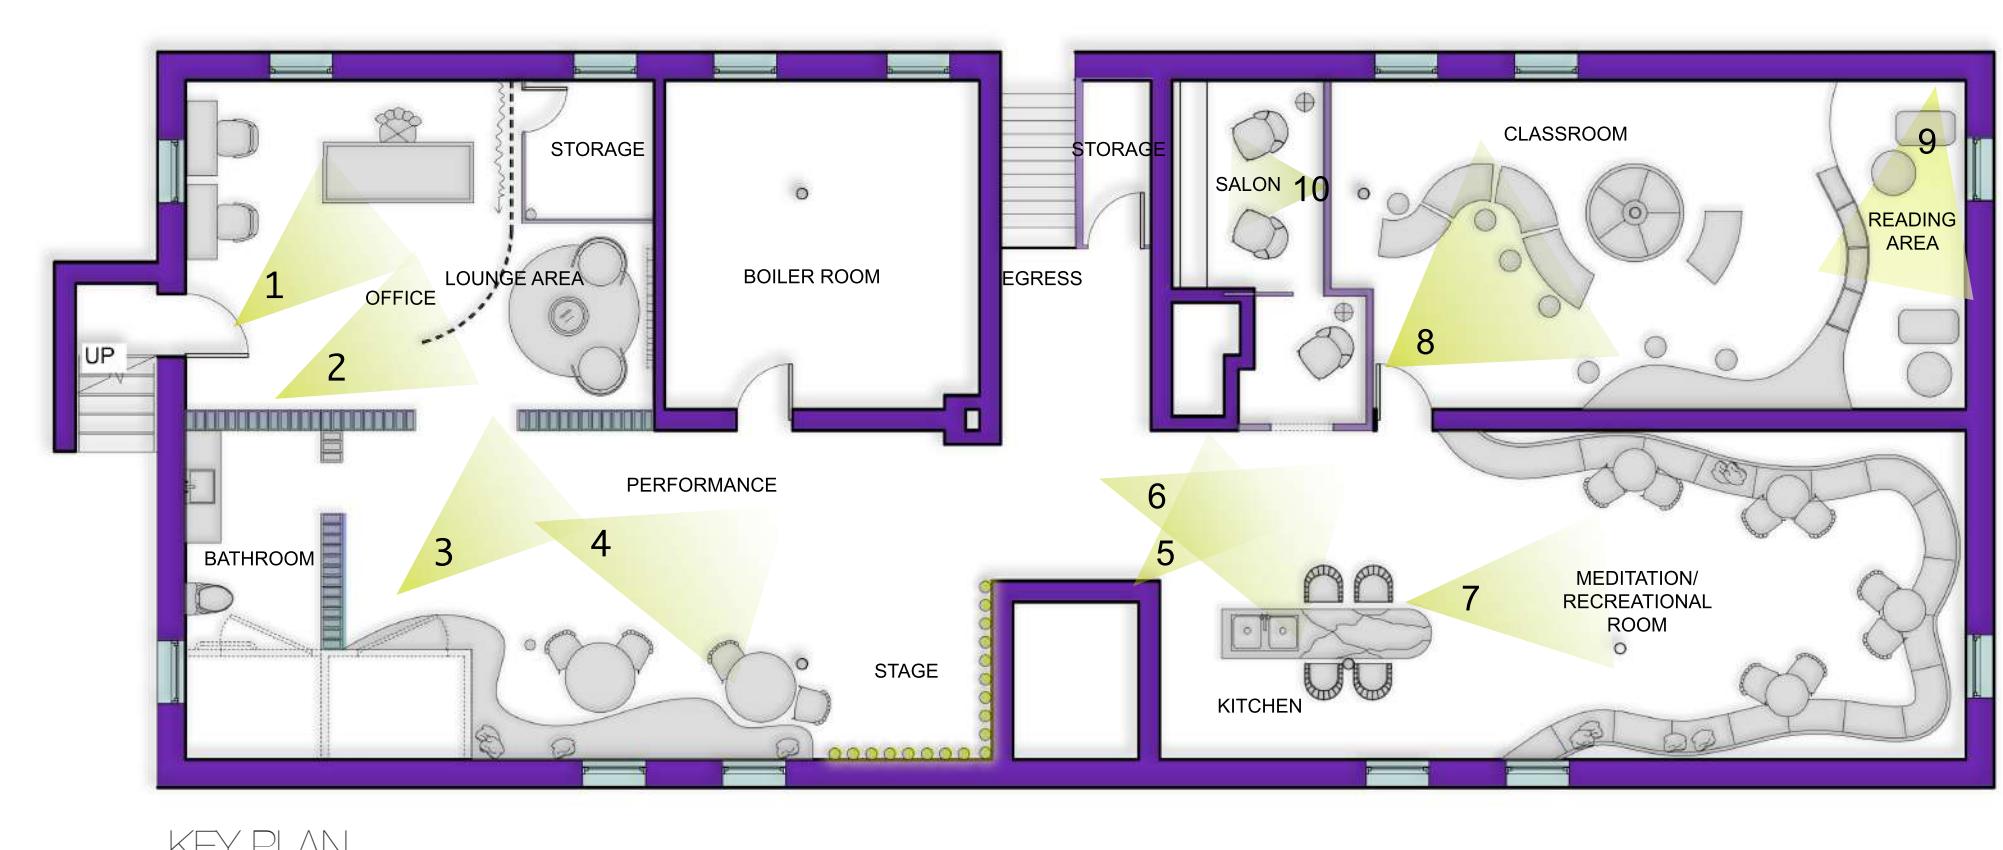


ELEVATION B-B' 1/4": 1'0"

CLASS ROOM

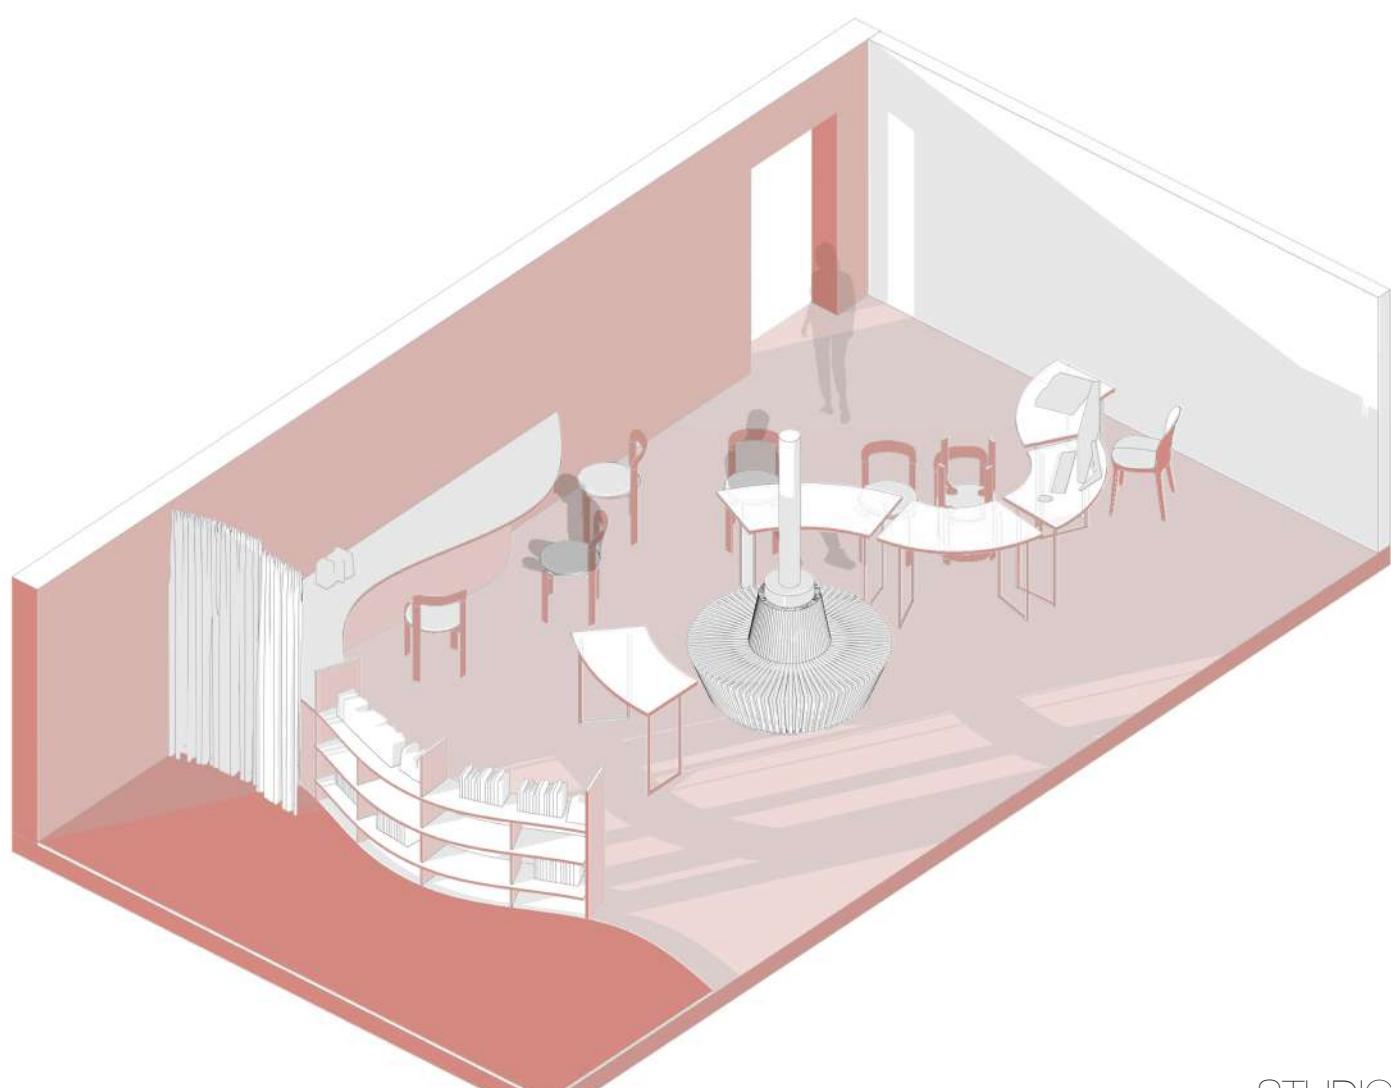

STUDIO

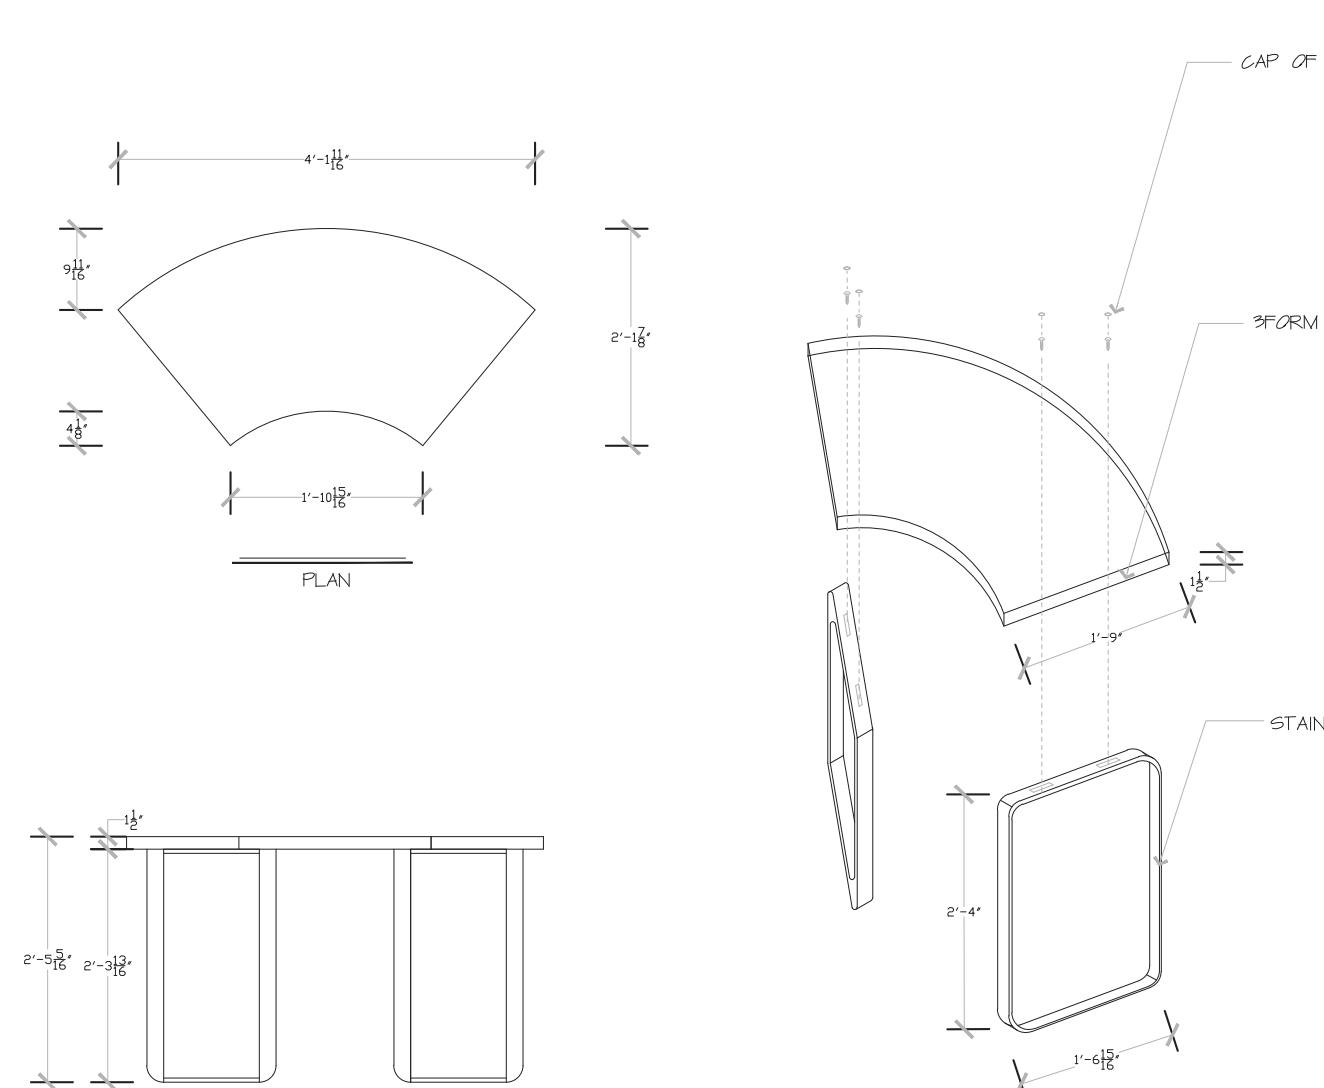

Multiprogramming and flexibility.
The semicircular design of the classroom desks allows multiple configuration.



PROJECTION




LECTURE




MAIN AREA


Multiprogramming and flexibility.
Grits Community can use the main area for parties, events and dining.

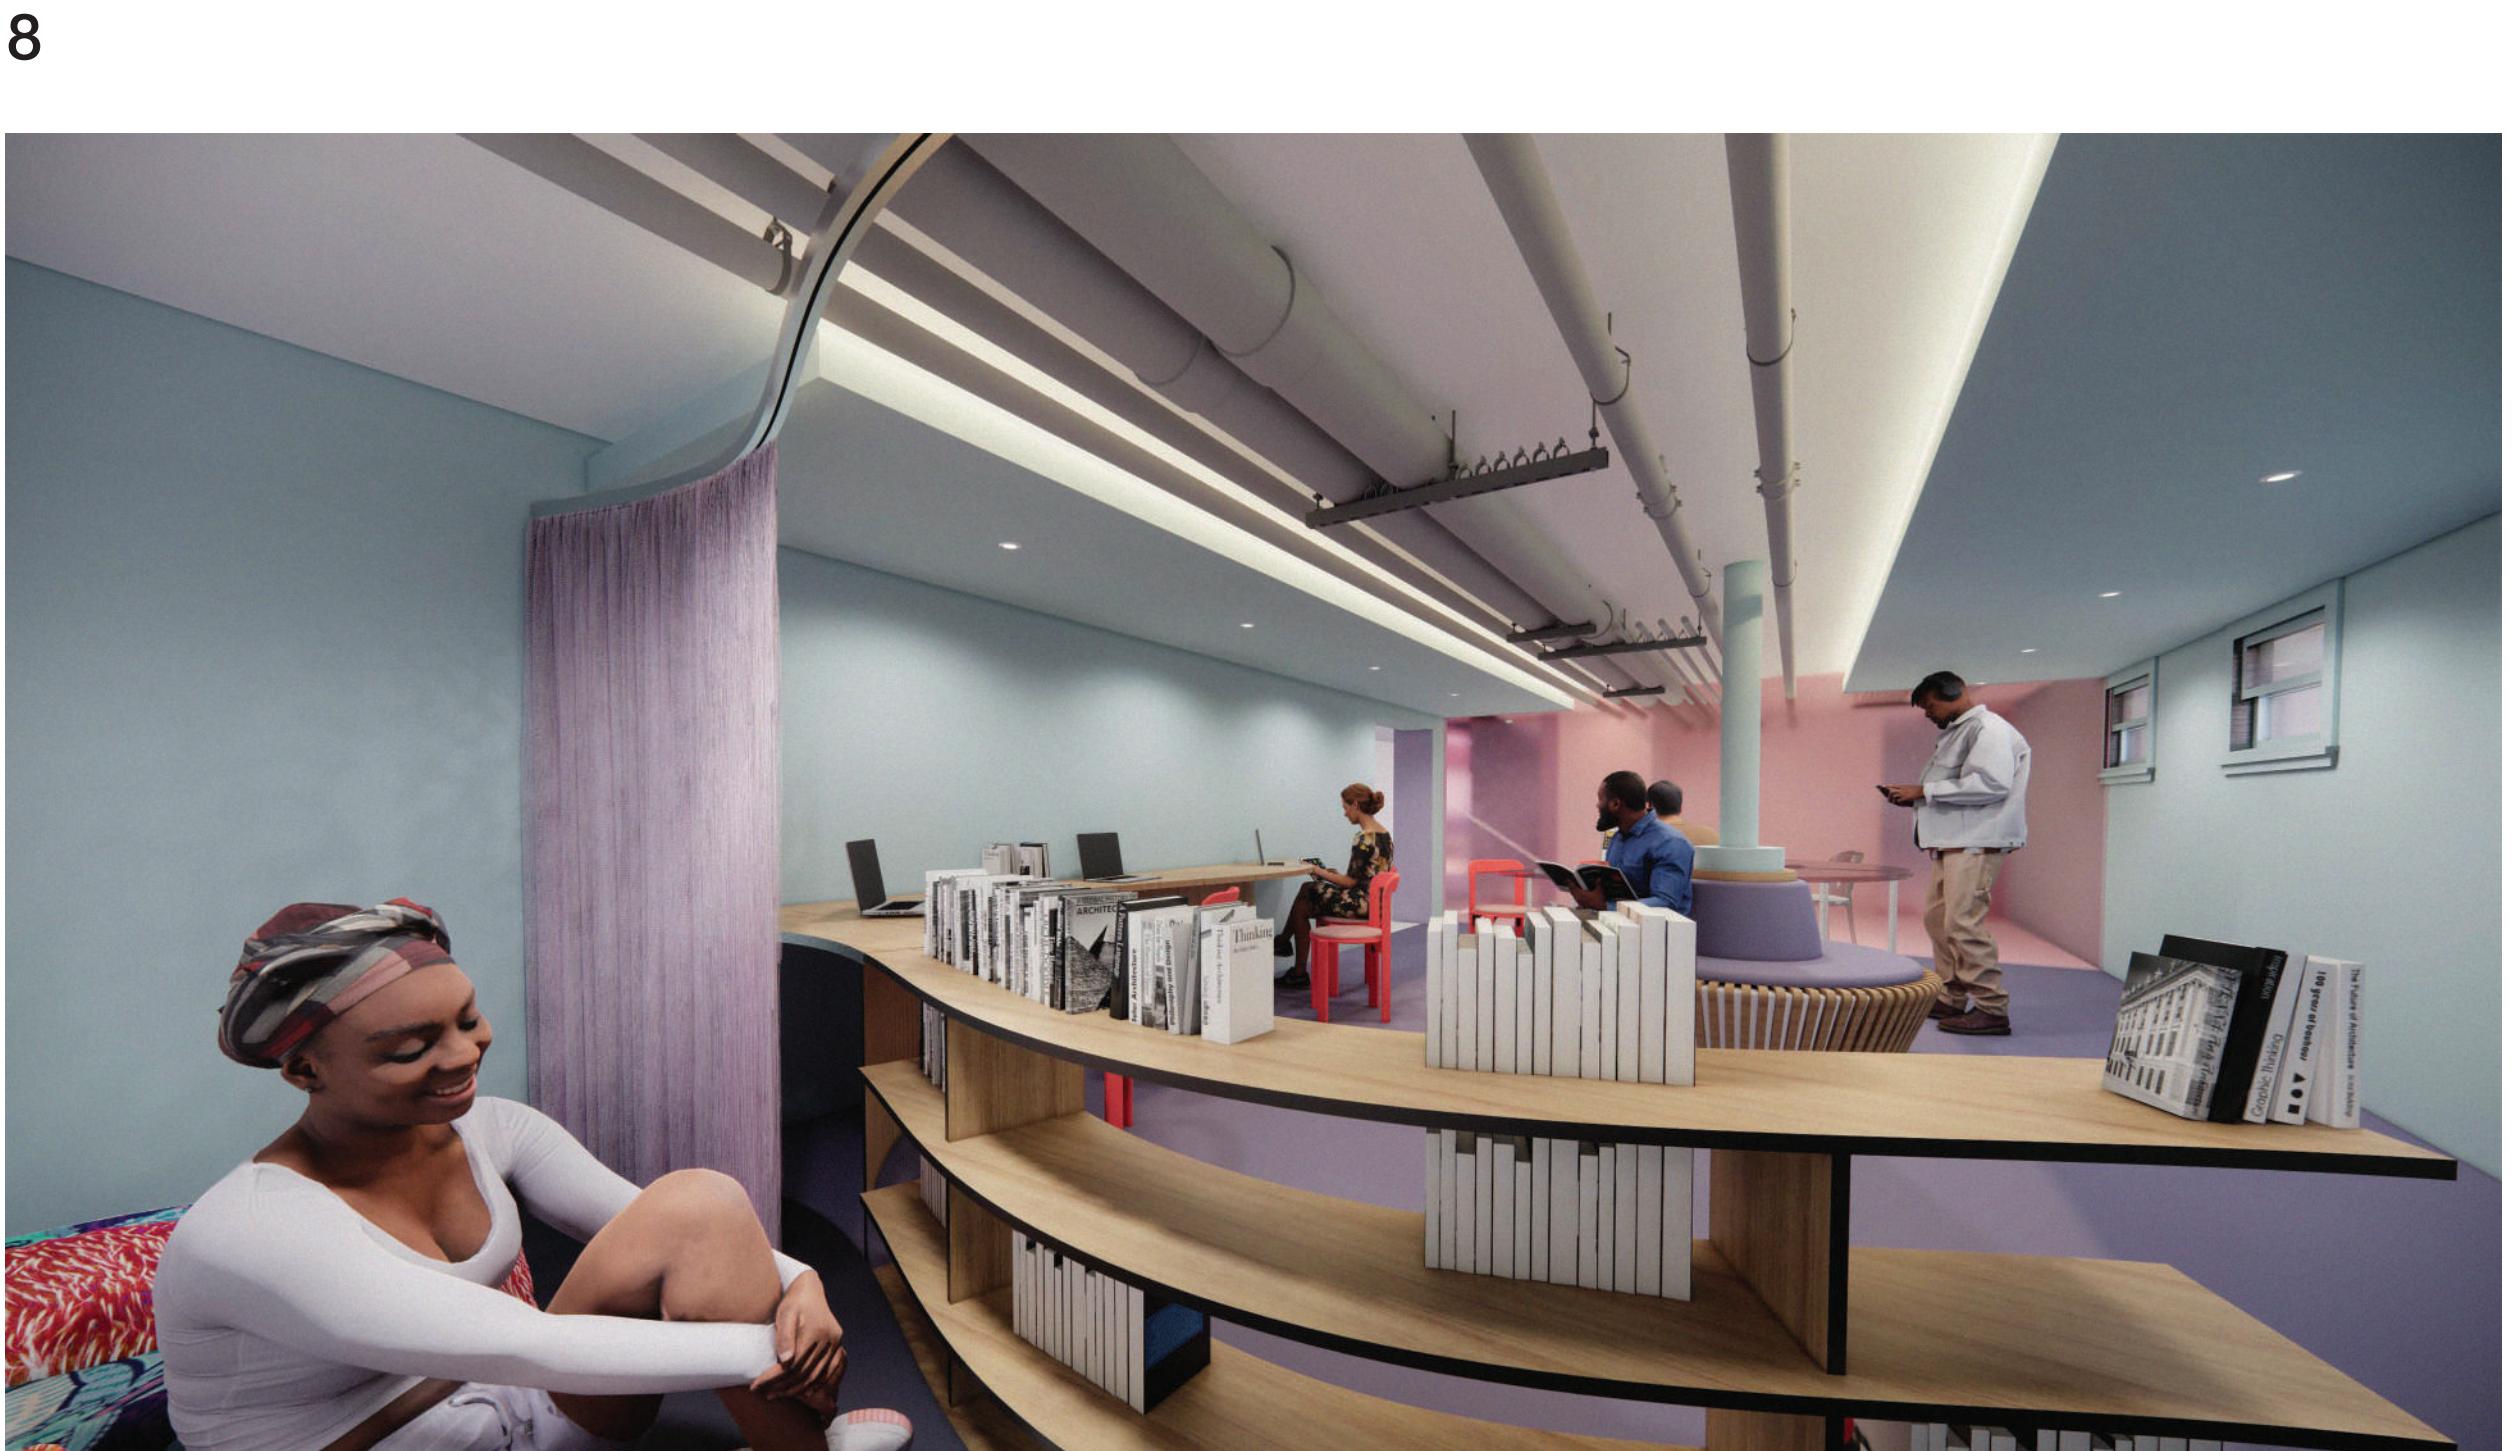


Reading area.
Semiprivate space.
The curtain gives privacy while allows you to see the classroom.

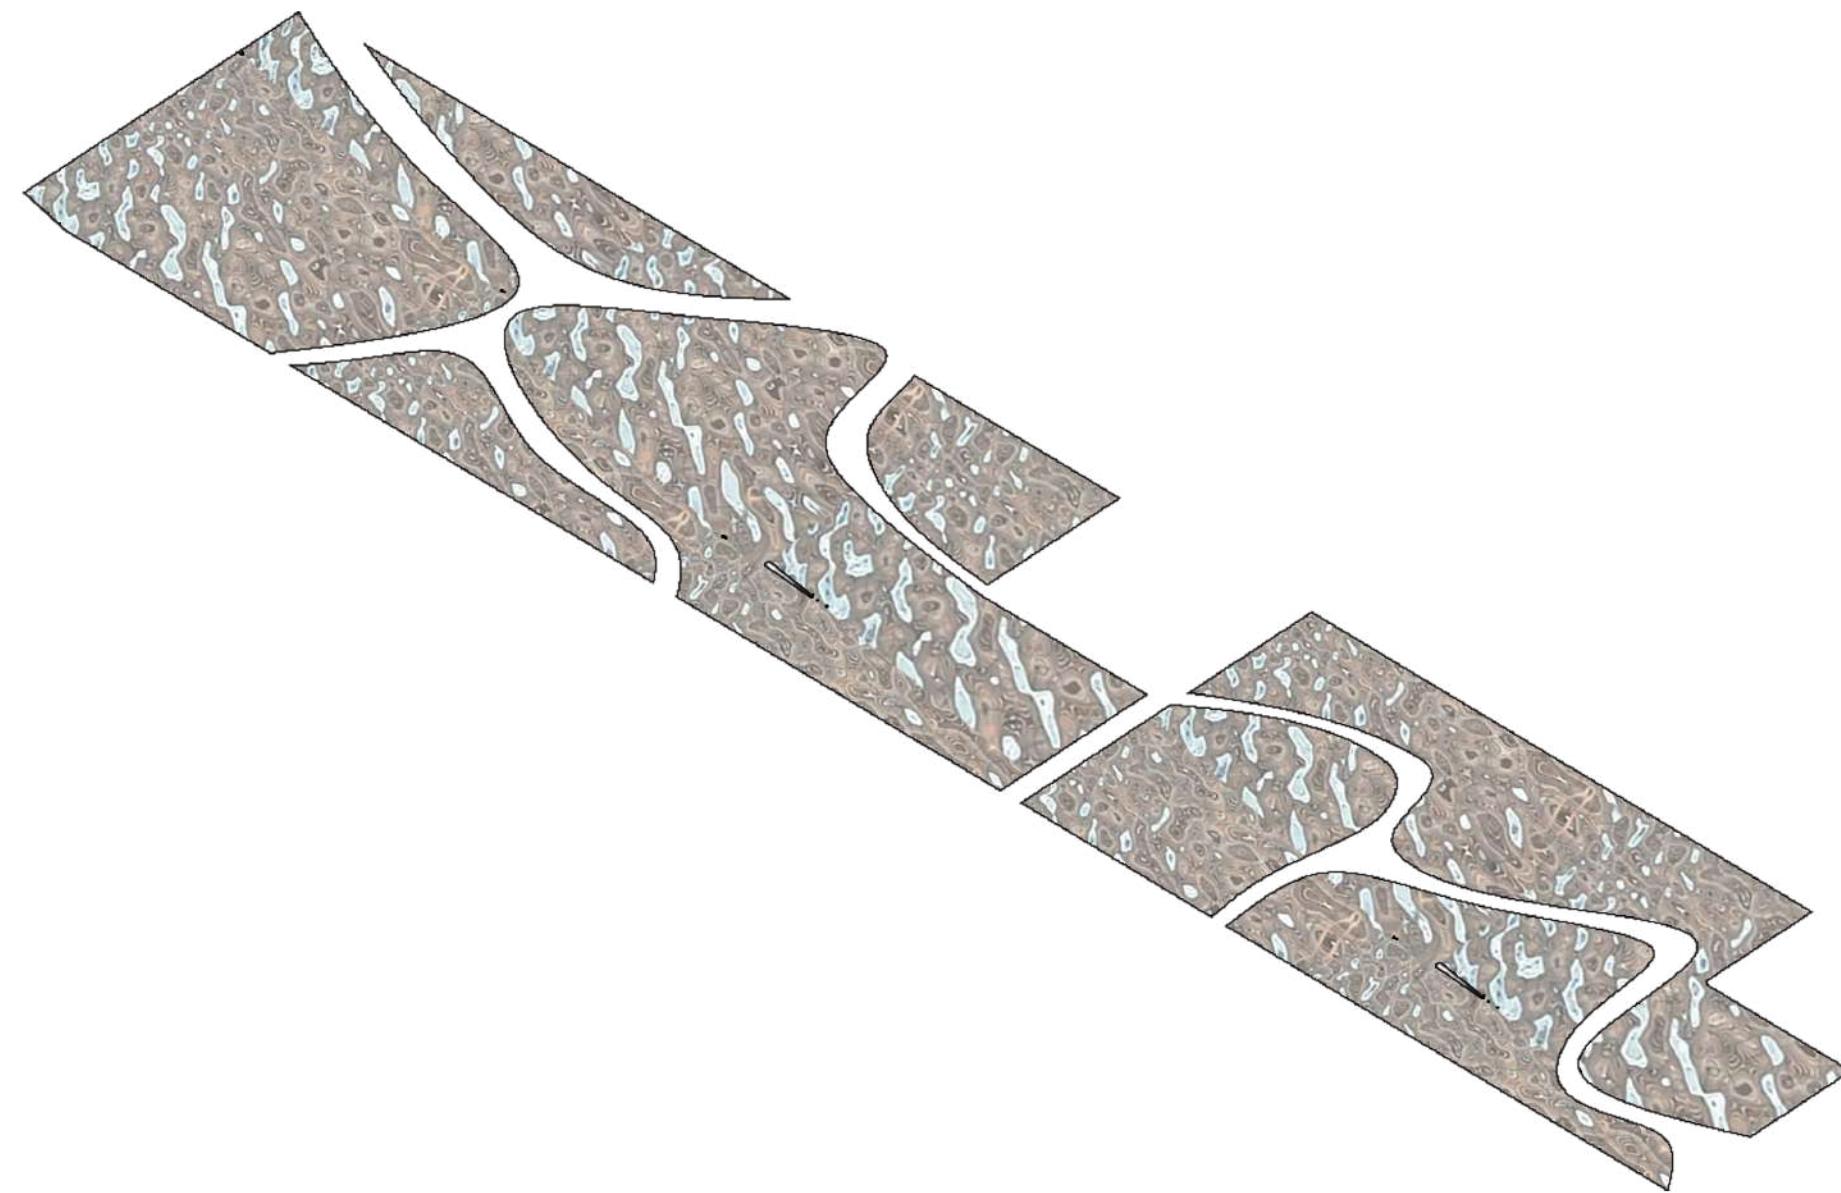


HAMMERED METAL CEILING SHEET

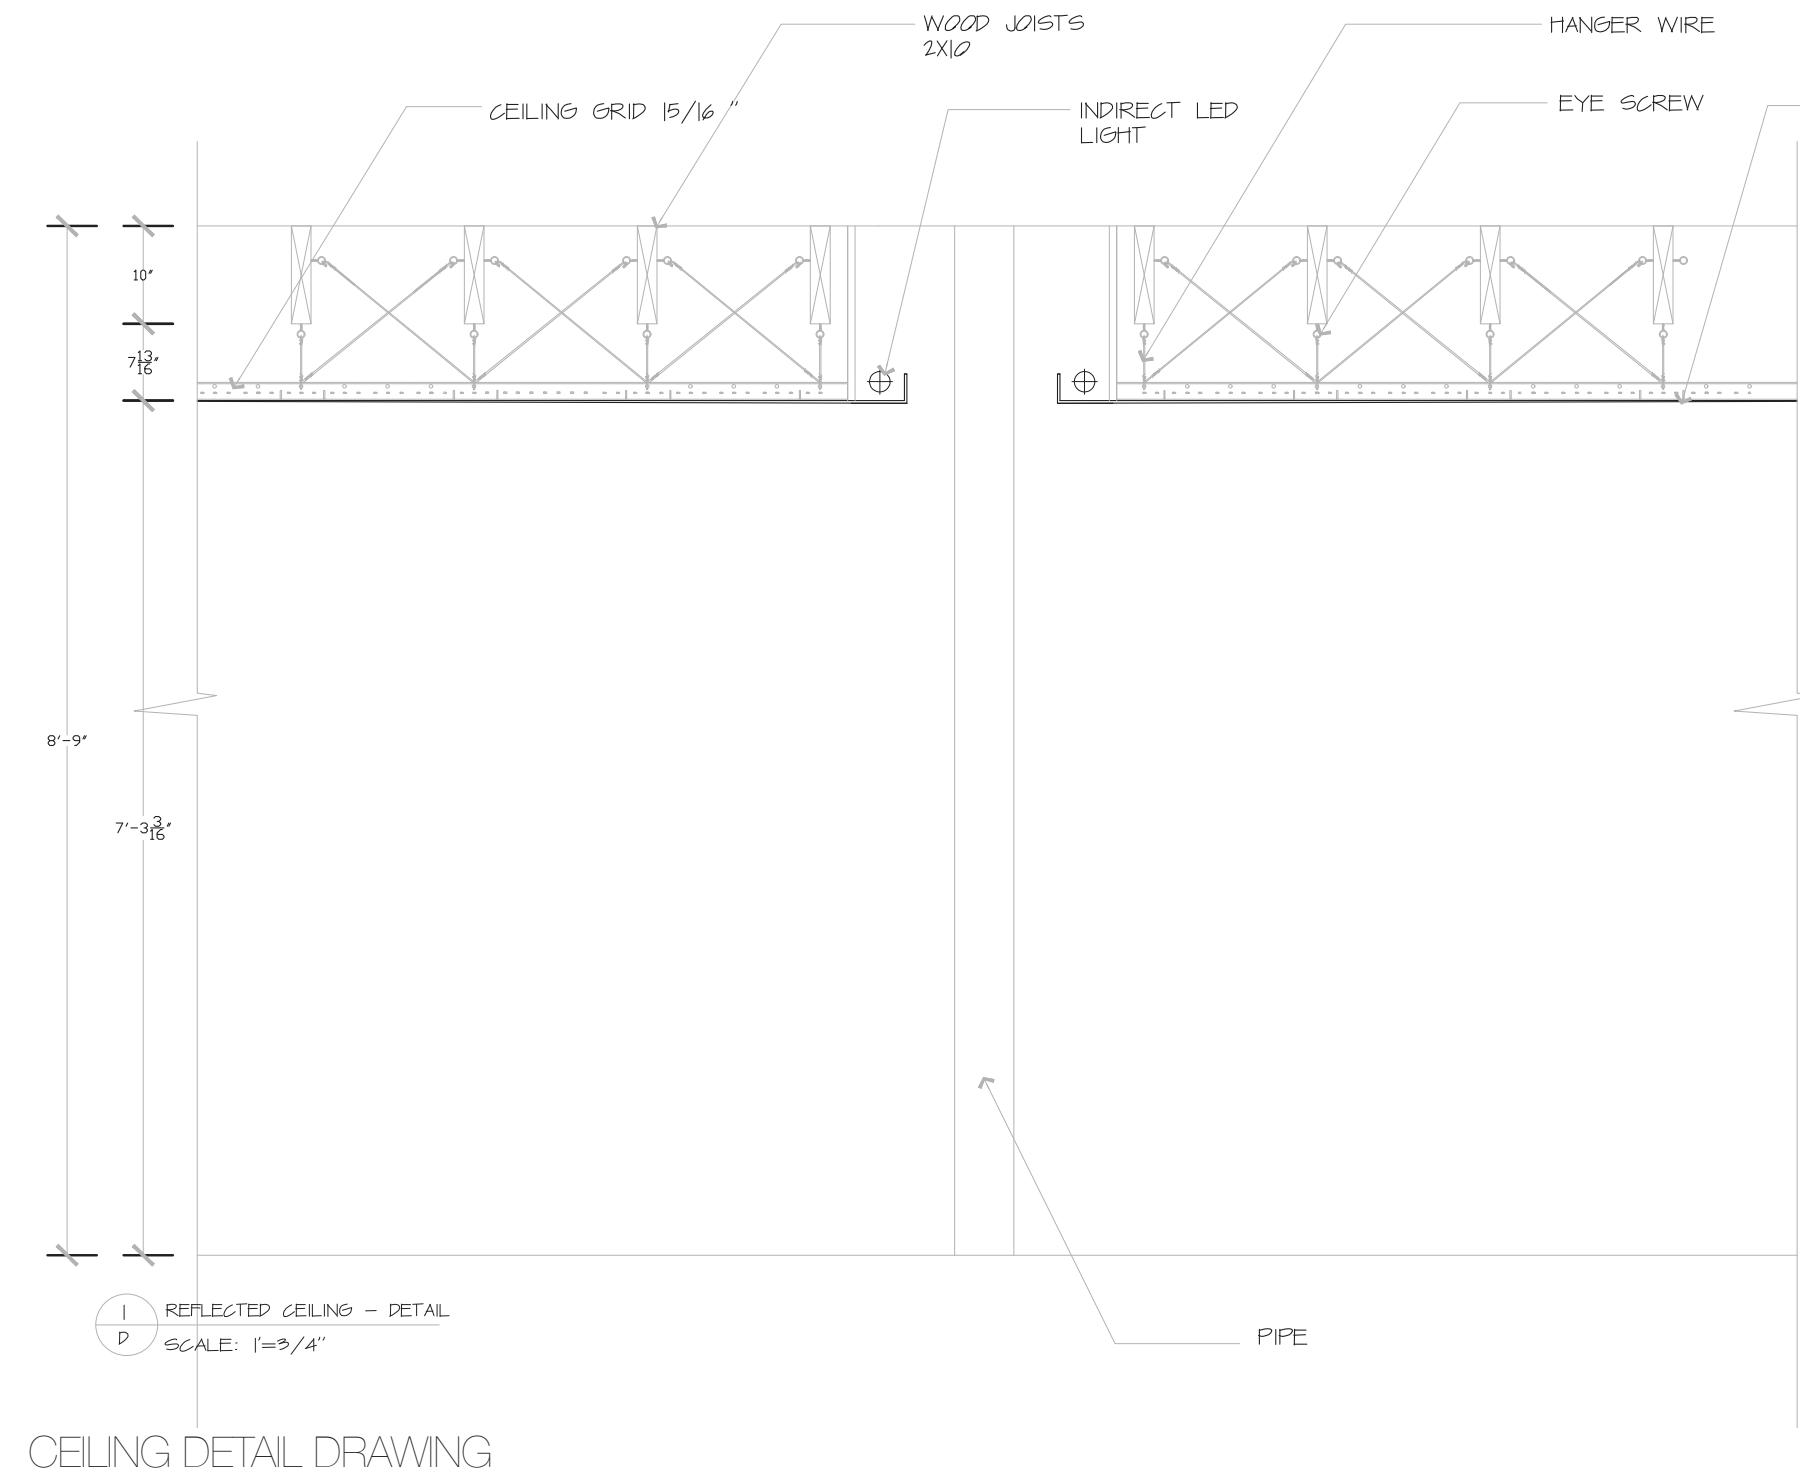


CEILING DETAIL DRAWING

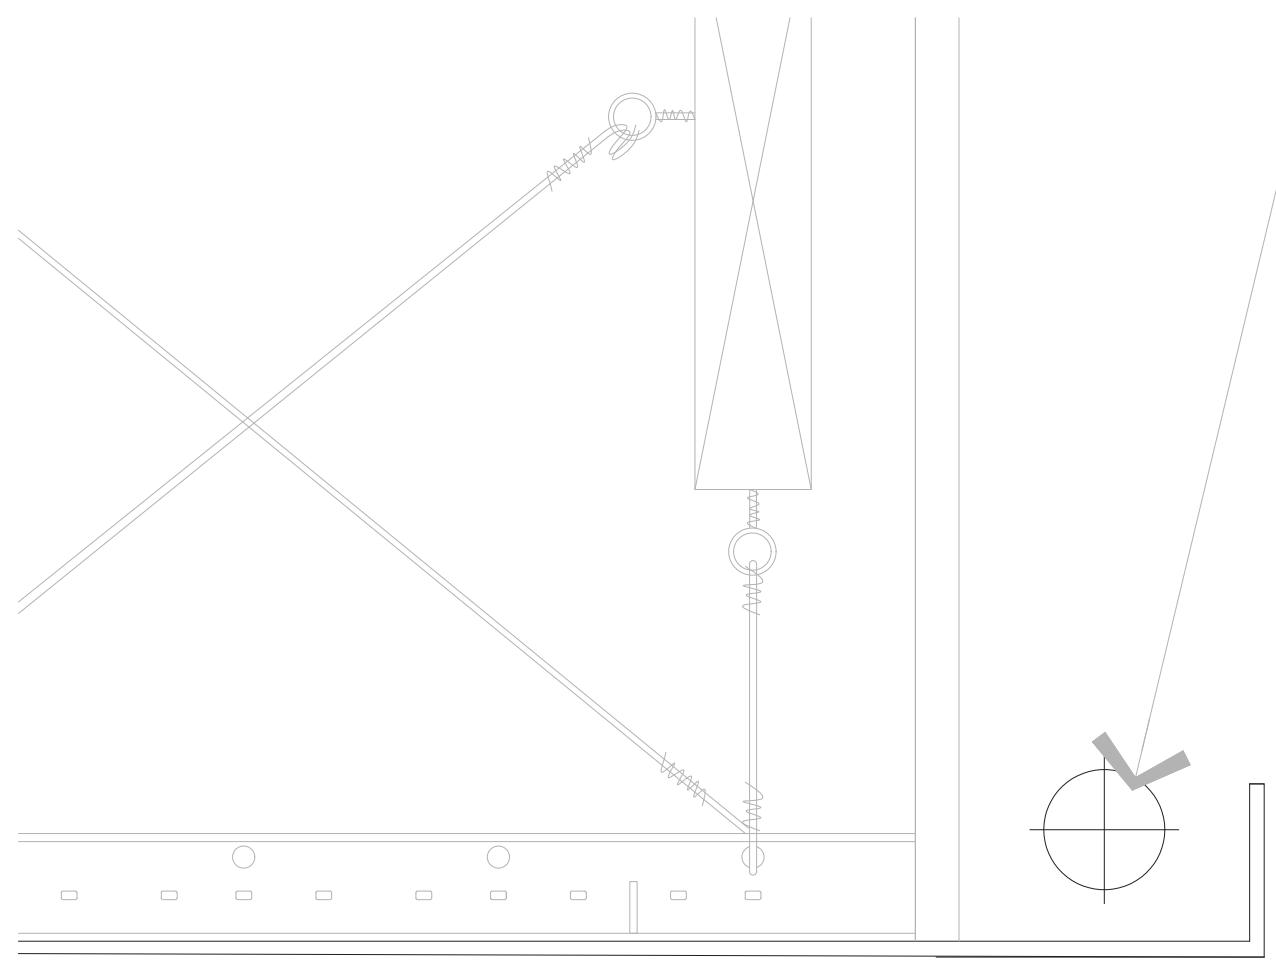

CEILING DETAIL DRAWING - CALLOUT

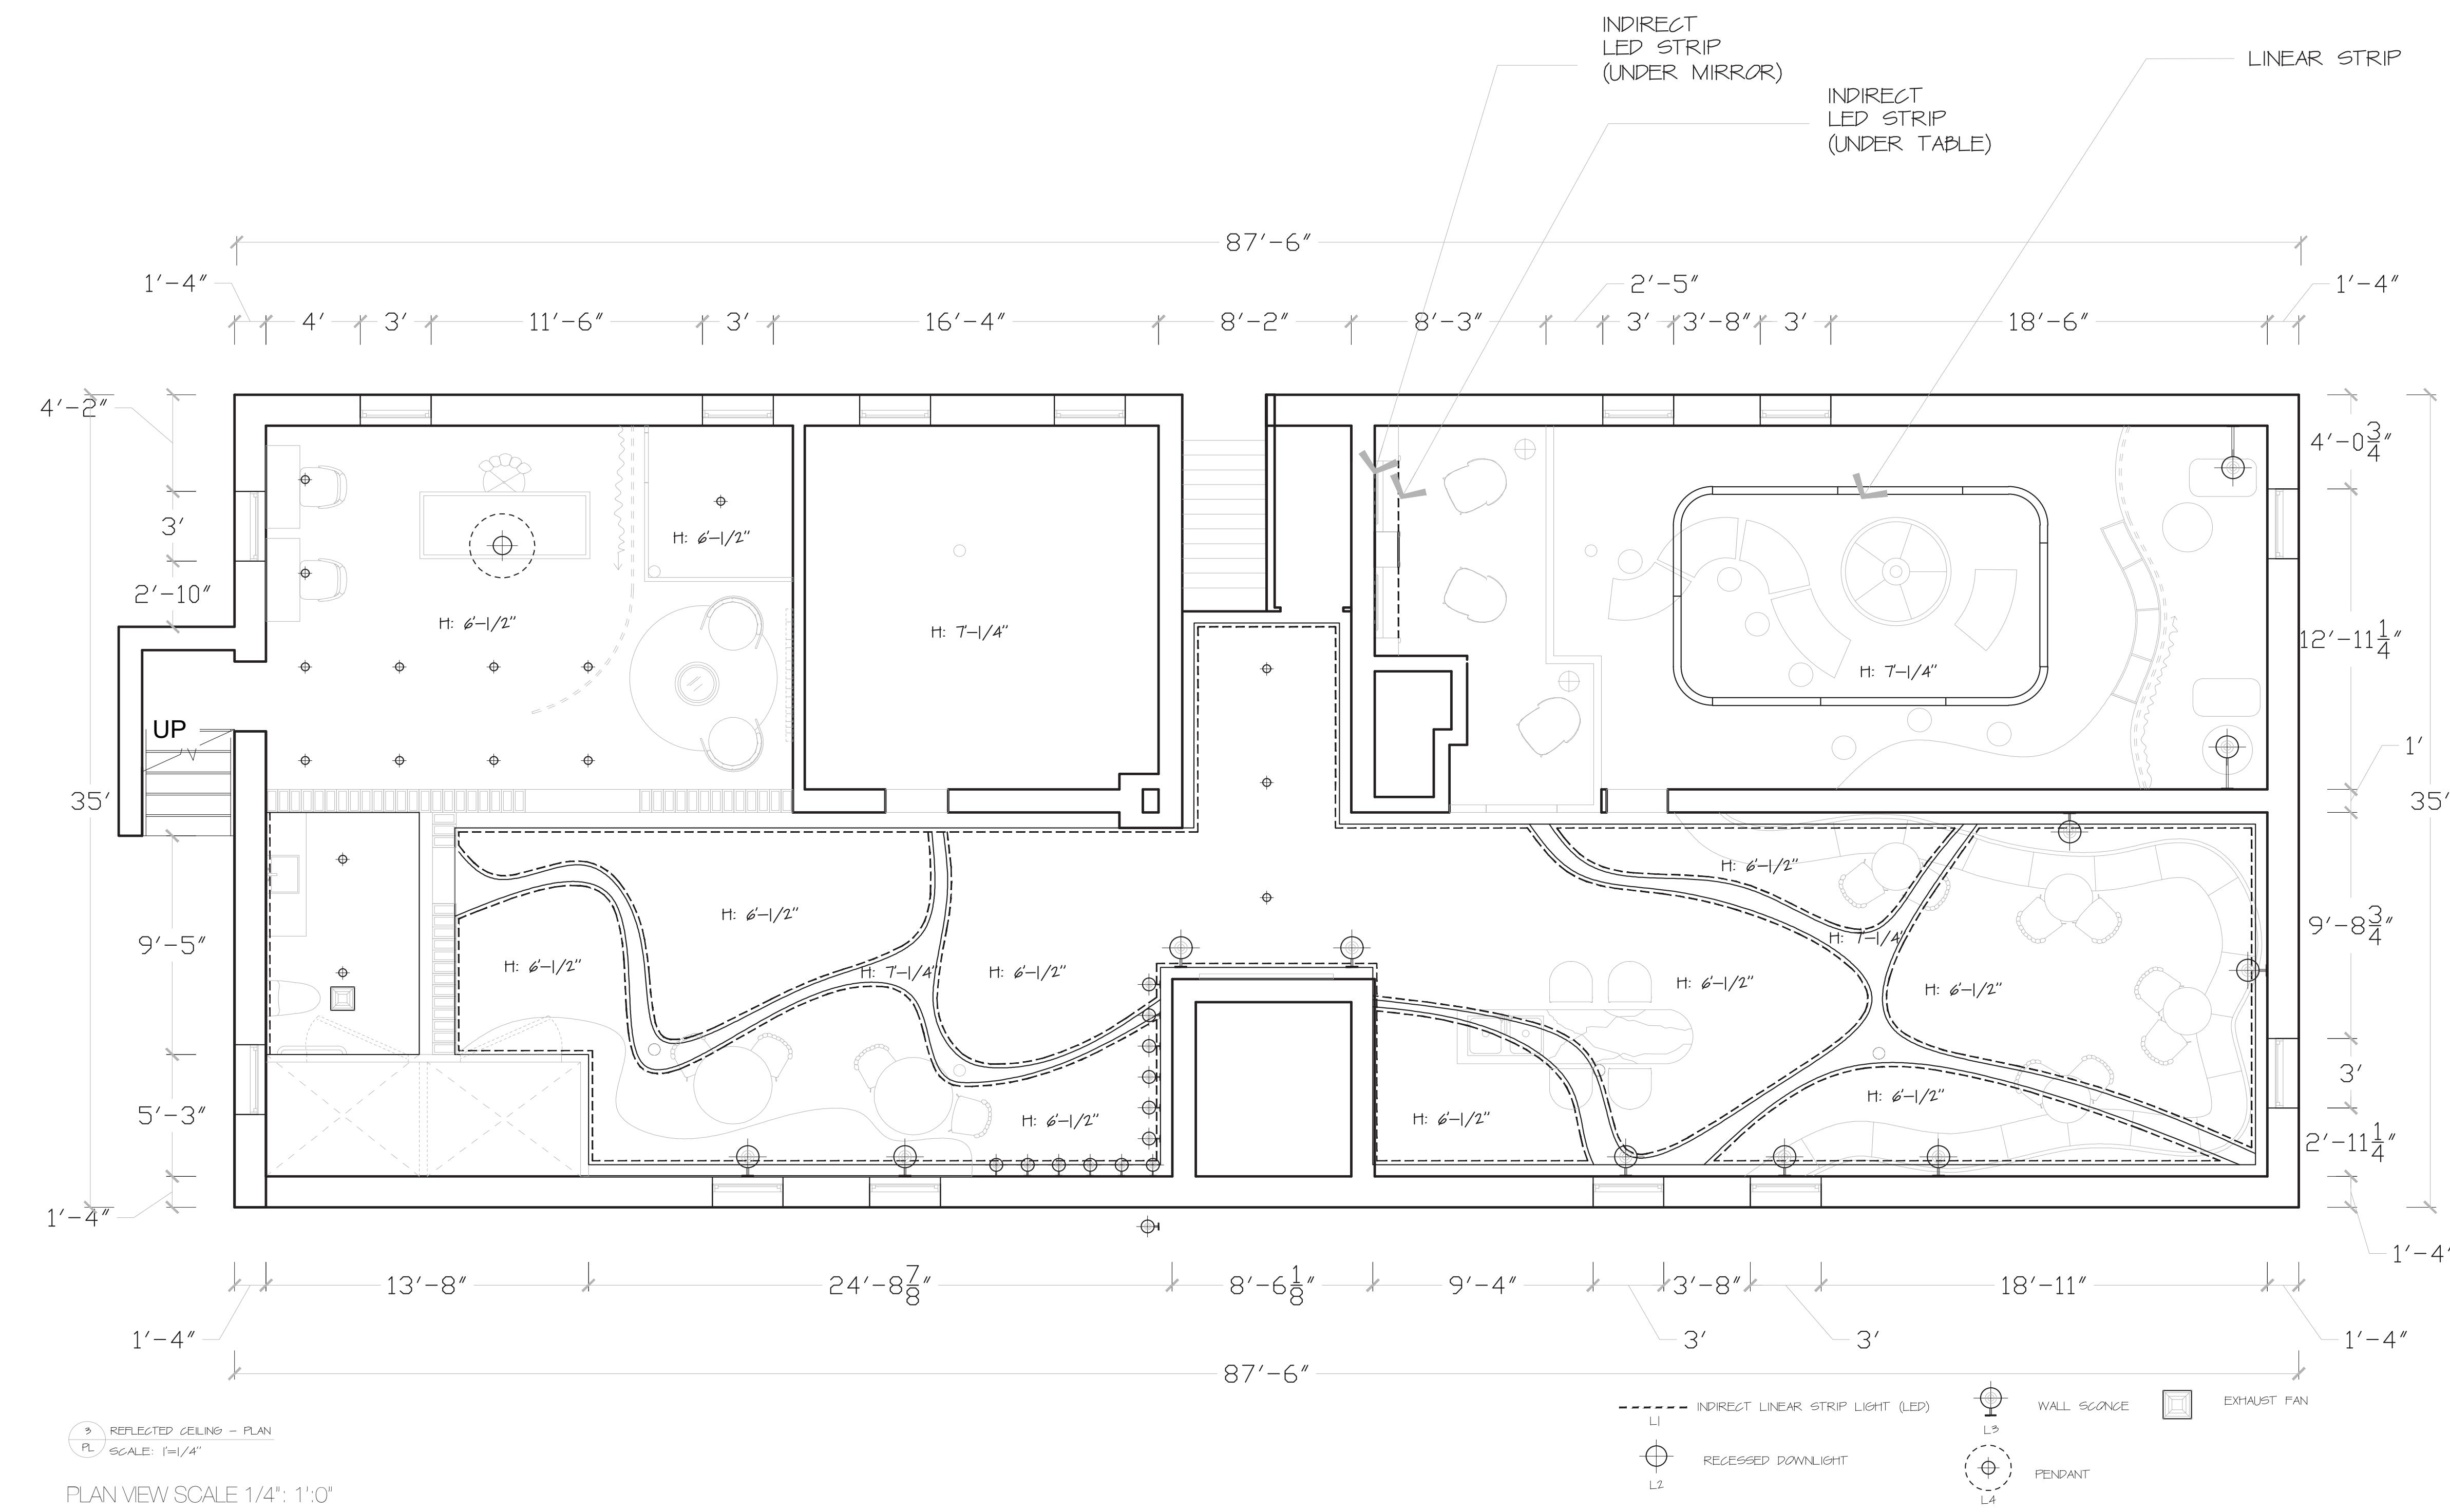

PL SCALE: 1'=1/4"

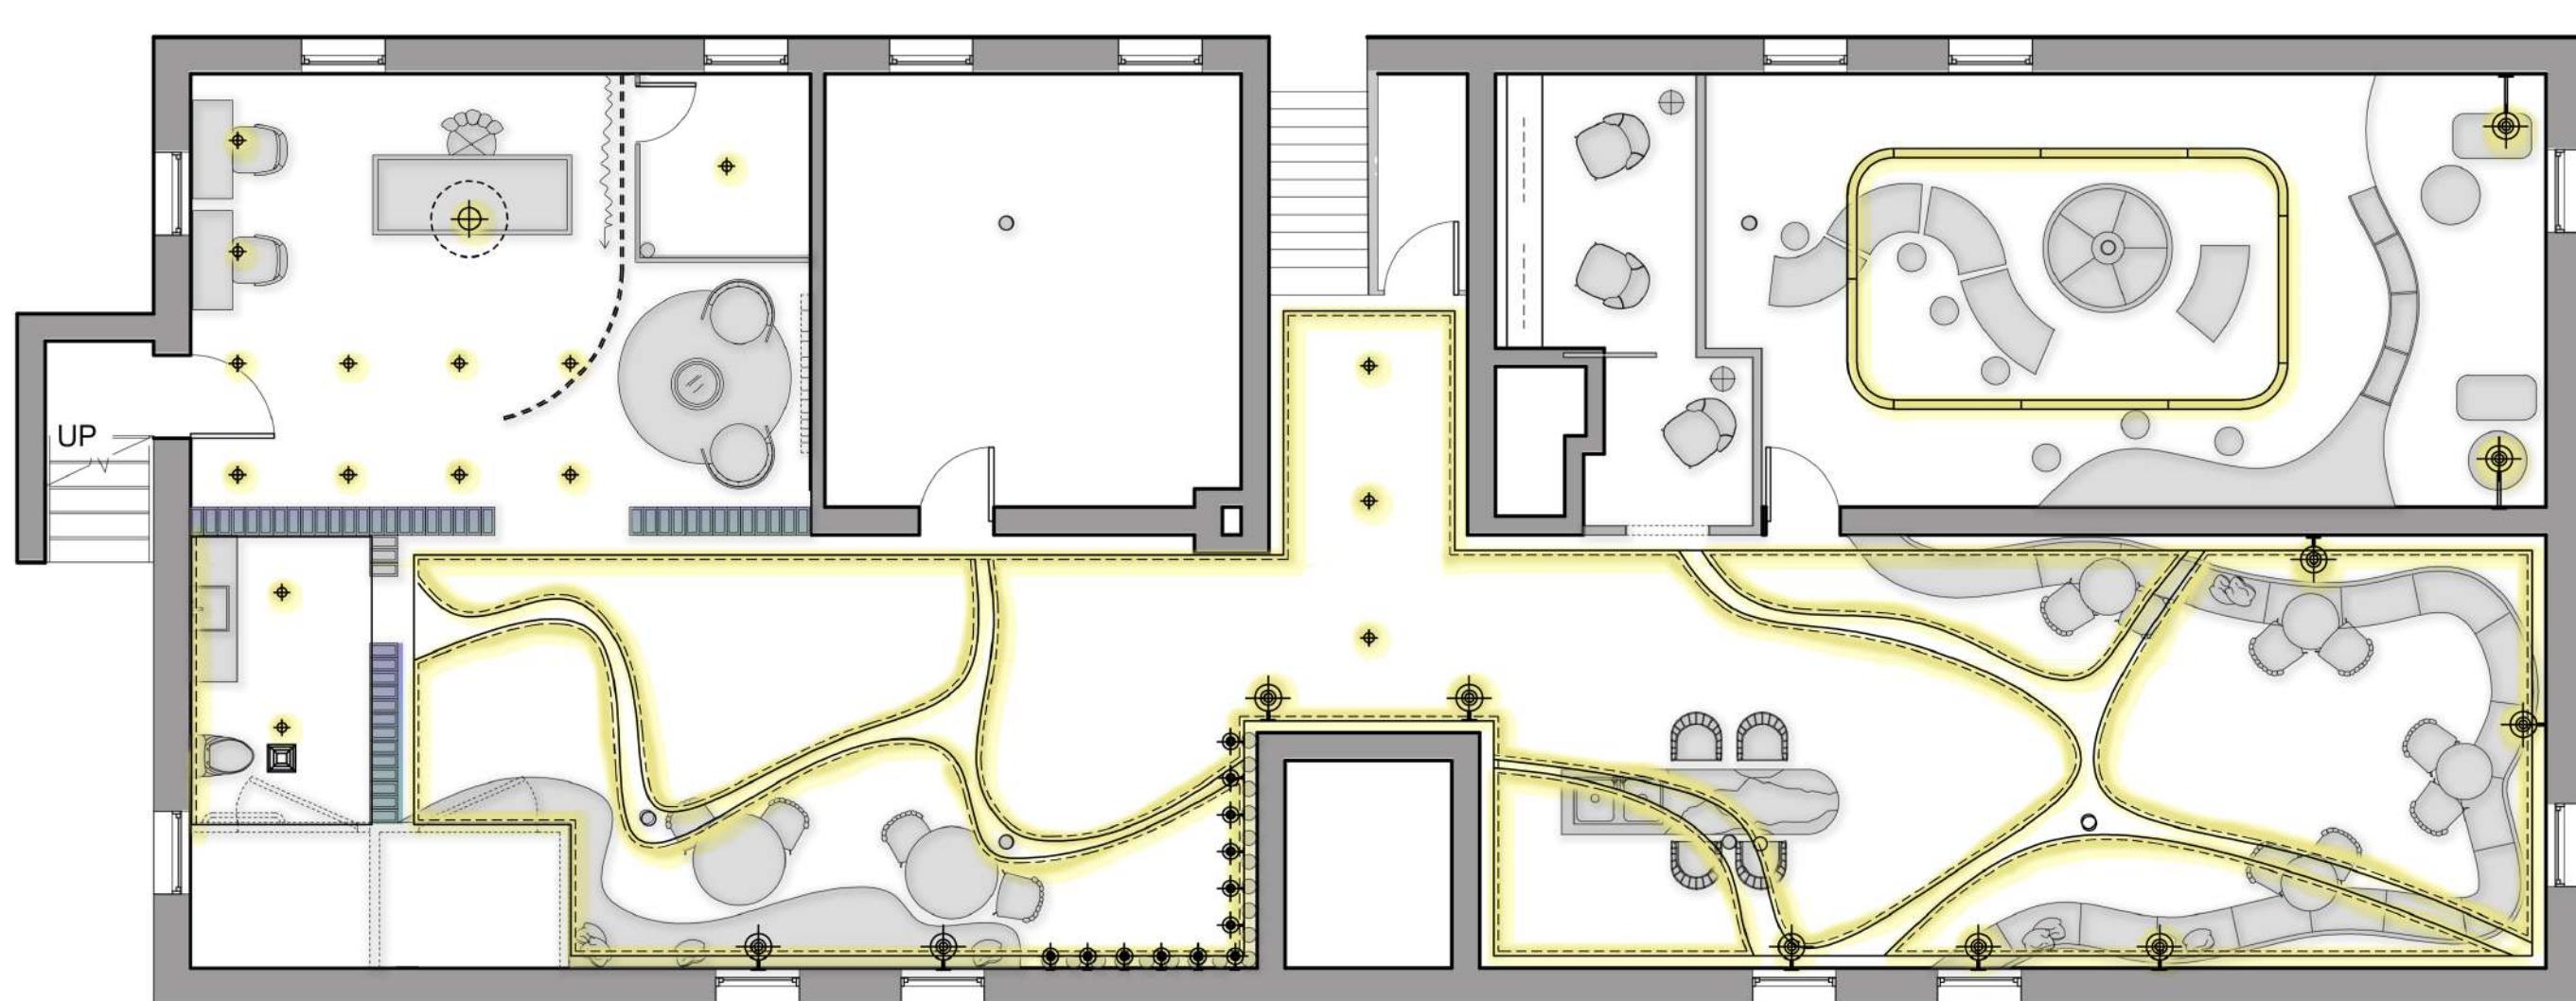


Lighting strategy.
Most of the light is recessed
in the ceiling.
Multiple wall sconces due to
the low high of the ceiling.
Dimmer multicolor light in the
yoga room.



6 11:00 PM DANCE PARTY | KITCHEN




5 SMALL SEMI -PRIVATE AREA. TRANSLUCENT DOOR

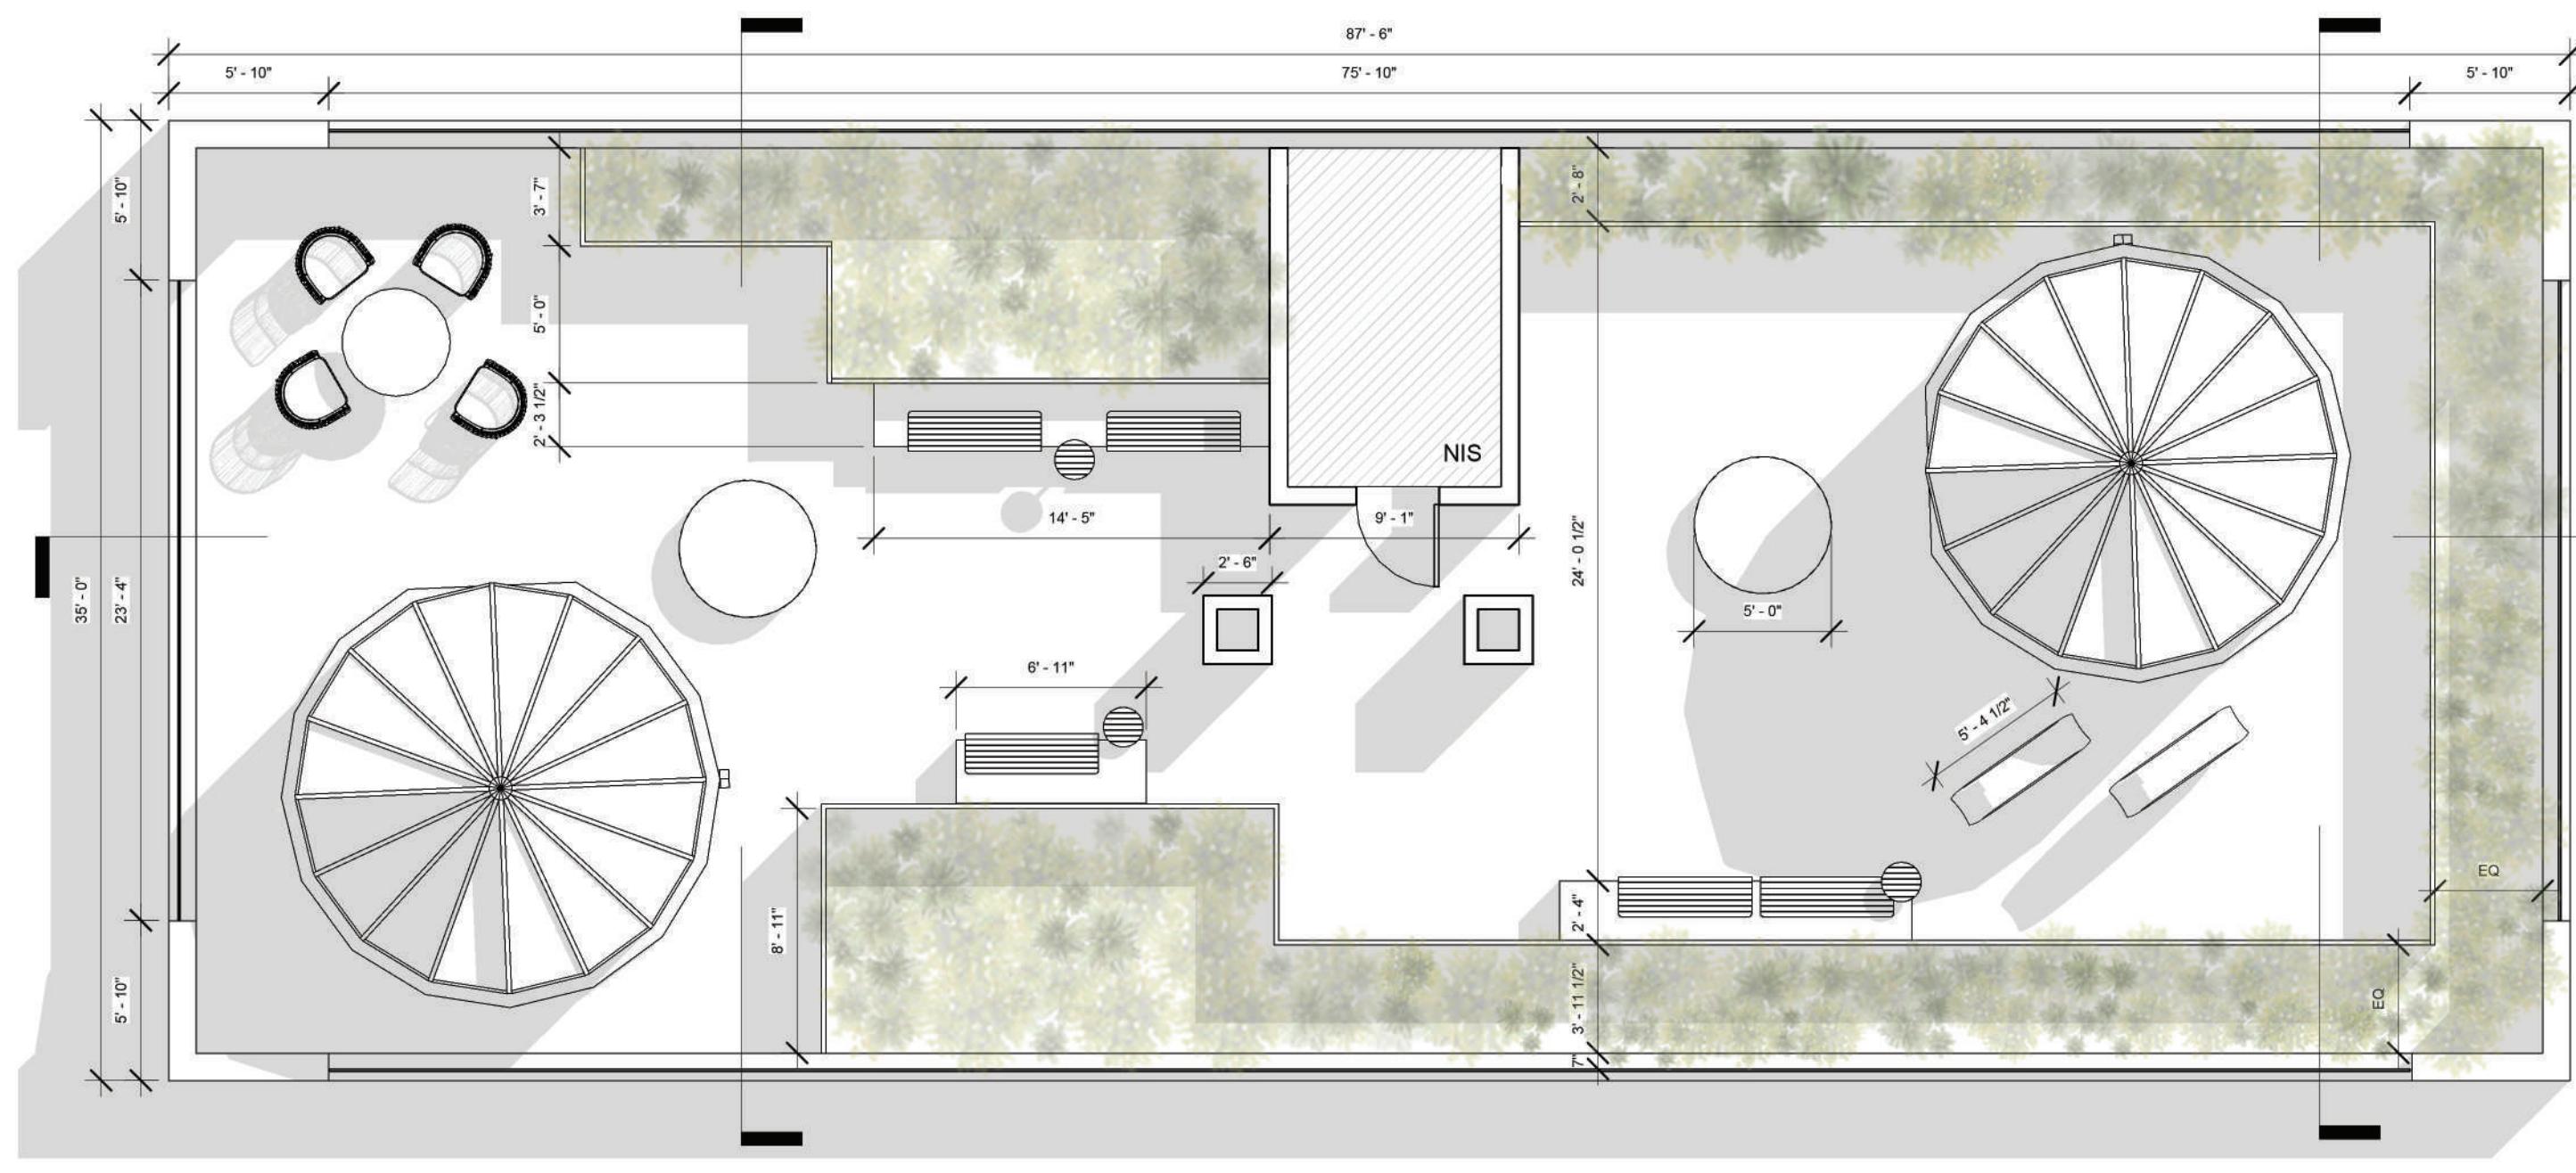

ROOFTOP PLAN



10 BEUTY SALON. REFLECTION OF THE TRANSLUCENT WALL

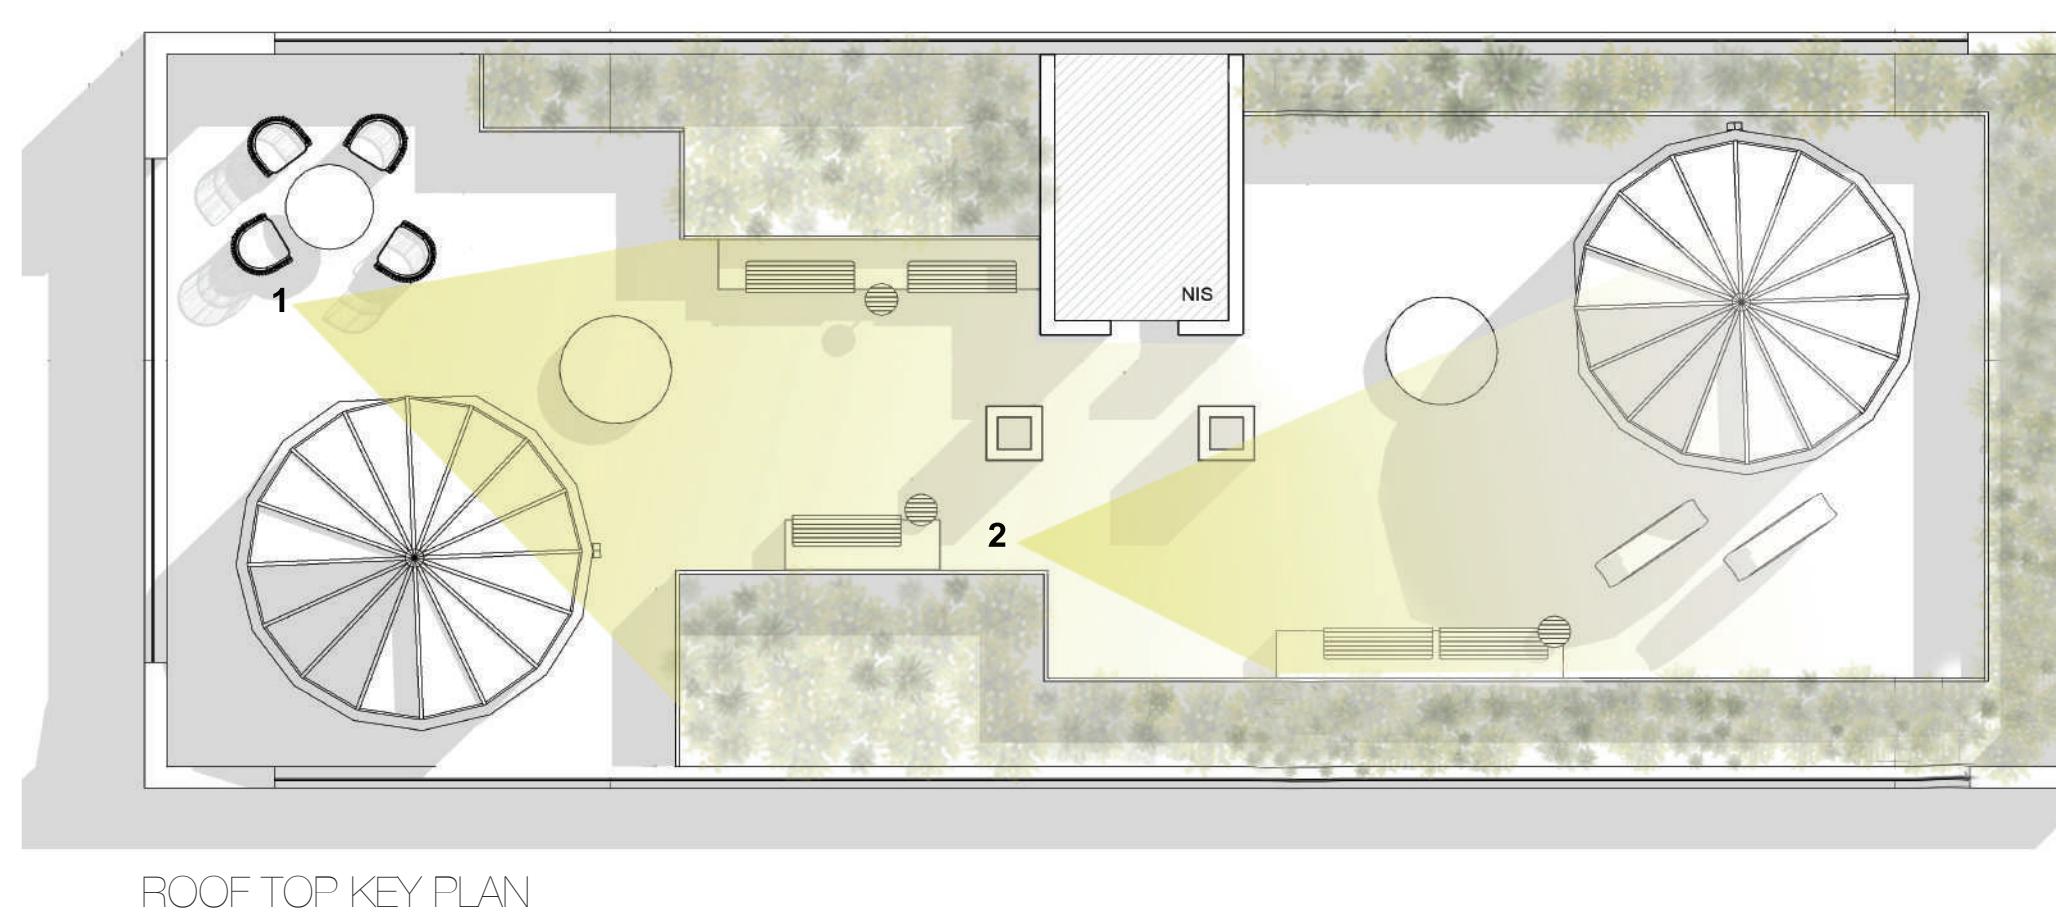

THE OFFICE

